

Инженерный комплект чертежей

Читаемые листы для предварительного согласования с архитектором, электриком, инженерами ОВ/ВК, газовой службой, мебельщиком и садовником.

СПДС-ориентированная подача. Статус: эскиз/координация. Газ, несущие изменения, электрика, ВК и ОВ не выдаются в монтаж до расчёта и подписи профильных специалистов.

РЕЕСТР


АР-04 Кухня-гостиная. Развёртки четырёх стен	ЭОМ-01 Кухня. Розетки и выводы
КМ-04 Кухня. Координация выбранных товаров	АР-05 Спальни. Сводный план мебели
АР-05.1 Спальня родителей. План мебели	АР-06 Спальня родителей. Развёртки
АР-05.2 Детская Дарины. План мебели	АР-07 Детская Дарины. Развёртки
АР-05.3 Детская Ярика. План мебели	АР-08 Детская Ярика. Развёртки
АР-09 Мангальная. План 1640×1990 и вид по фото	ОВ-01 Котельная. План и развёртки
ОВ-02 Вентиляция. Принципиальная схема	ГП-01 Посадочный план

ОСНОВА	PDF заказчика, листы 6-11; изменения по балкону, мангальной и участку.
ЕДИНИЦЫ	мм; участок 20×30 м; дом по осям 14,10×11,46 м.
ПРОВЕРИТЬ	Натурные обмеры, отметки, конструкции, мощности и инженерные расчёты.


КМ-20.02 · Кухня — четыре развёртки стен

Вариант А · отметки от чистого пола (AFFL) · горизонтальные привязки от левого чистового угла каждой развёртки


ЮЖНАЯ СТЕНА S · рабочая линия 5530

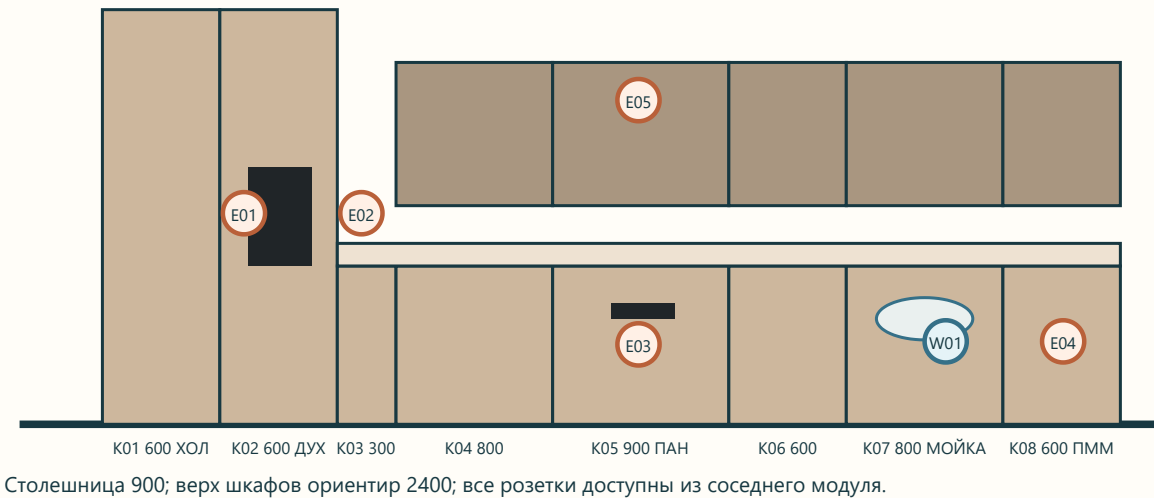

СЕВЕРНАЯ СТЕНА N · заднее остекление

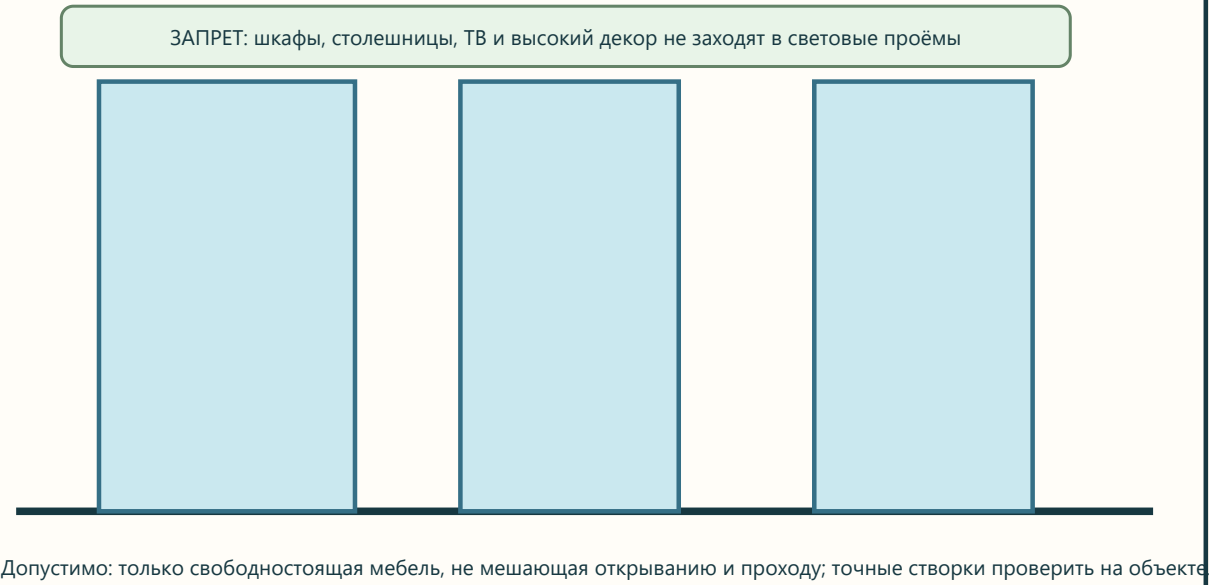

ВОСТОЧНАЯ СТЕНА E · боковое окно и проход

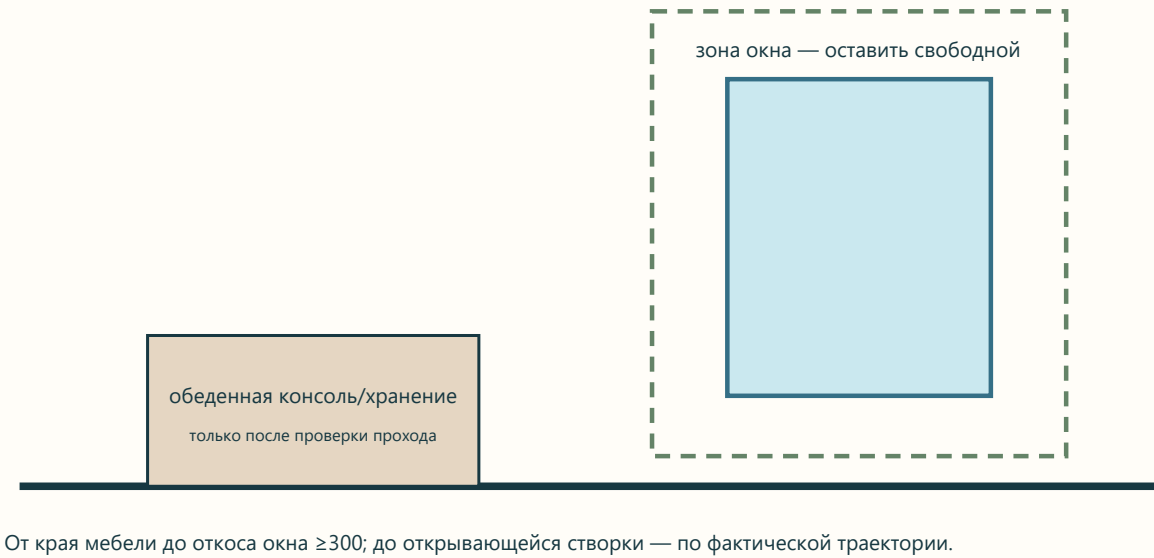

ЗАПАДНАЯ СТОРОНА W · связь с гостиной



АР-04

Кухня-гостиная. Развёртки четырёх стен · источник графики: связанный координационный лист

СТАТУС


Эскиз/координация. Размеры подтвердить обмером и профильным расчётом.

ВЫПУСК

v20.2
30.07.2026

ЭОМ/ВК-20.01 · Точные точки кухни — задание мастерам

Вариант А · X — от левого чистового торца линии 5530 · Z — центр точки от чистого пола · все значения предварительные до паспортов техники

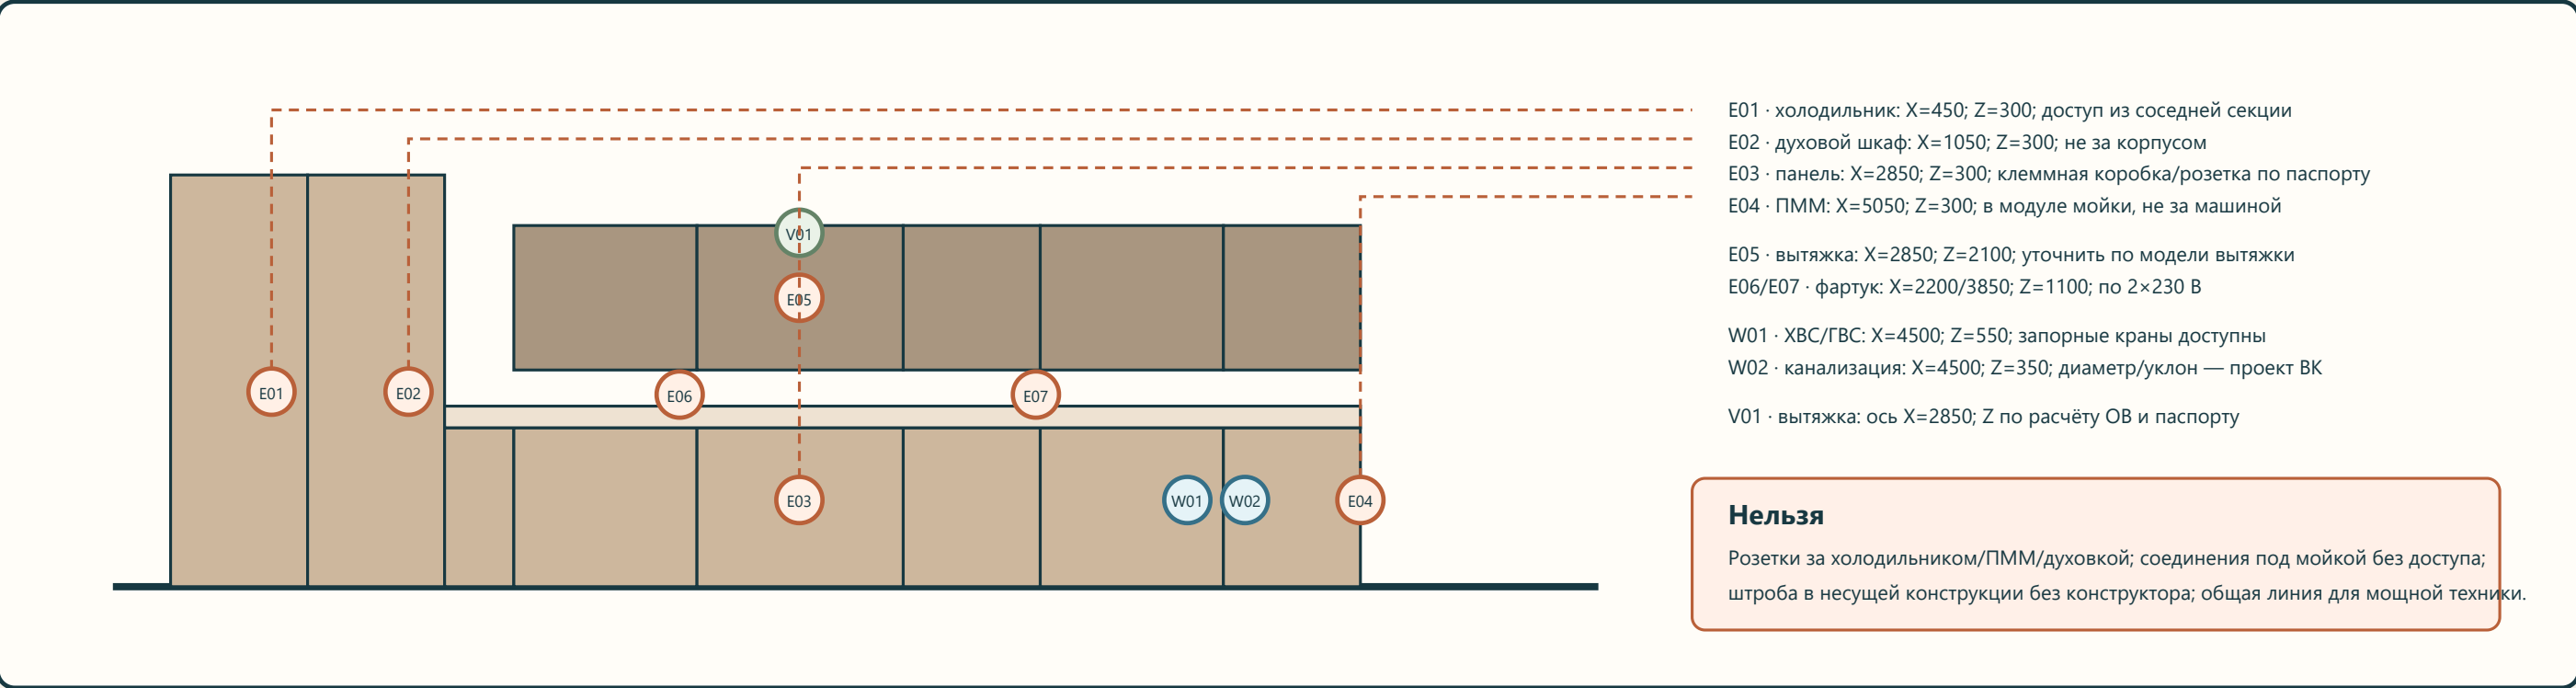

Реестр точек и задание электрику

E01	Холодильник	450	300	в соседнем сервисном модуле	отдельная рекоменд.; расчёт ЭОМ	паспорт, шнур, вентиляционные зазоры
E02	Духовой шкаф	1050	300	в соседнем модуле, доступ спереди	отдельная; кабель/автомат по расчёту	мощность, тип вилки/клемм
E03	Индукционная панель	2850	300	в соседней секции, не под горячей зоной	отдельная линия; мощность ориентир 7 кВт	точная модель и схема производителя
E04	Посудомоечная машина	5050	300	в модуле мойки, выше дна, сервисный доступ	отдельная рекоменд.; УЗО/диф — расчёт	шланги, аквастоп, зона возможной протечки
E05	Вытяжка	2850	2100	за декоративным коробом, доступ через шкаф	группа кухни; уточнить ЭОМ	высота установки и сечение канала
E06–E07	Фартук, 2 блока по 2 розетки	2200/3850	1100	не ближе горячей/мокрой зоны по нормам	2 группы по расчёту нагрузки	чайник, кофемашина, миксер, свободная точка
W01–W02	Мойка: ХВС/ГВС/слив	4500	550/350	краны, фильтр и сифон доступны	диаметры и уклон назначает ВК	ось мойки, измельчитель, фильтр, ПММ
S01	LED рабочей поверхности	по шкафам	1450–1650	БП в доступном шкафу, не замуровывать	отдельное управление L02	профиль, мощность ленты, охлаждение БП

Важно: окончательные кабели, автоматы, УЗО/дифзащита, уравнивание потенциалов и IP назначает лицензированный проектировщик ЭОМ по фактической мощности и действующим нормам.

ЭОМ-01
Кухня. Розетки и выводы · источник графики: связанный координационный лист

СТАТУС
Эскиз/координация. Размеры подтвердить обмером и профильным расчётом.

ВЫПУСК
v20.2
30.07.2026

КМ-04. Кухня 5200 мм — координация по выбранным товарам

Размеры в мм. Основание: реестр товаров v21, PDF лист 7 и связанный AP-04. Чистовые размеры и монтажные вырезы подтвердить.

1. Фасад нижней линии · общая ширина 5200




Цветом выделены товары с зафиксированным паспортным габаритом. Доборы: 330 мм суммарно после чистового обмера стены 5530.

3. Паспортные ниши и вырезы — согласовать с мебельщиком

Код	Товар	Корпус	Модуль	Стоп-проверка
K-01	CVI594SBG	590×520×58	900	вырез только по монтажной схеме
K-02	EOEM.769S1	595×575×595	600-колонна	розетка рядом, не за корпусом
K-03	MBF177SWGR	540×545×1775	600-колонна	ниша и вентиляция по паспорту
K-04	MLP60530	598×550×815	600	цоколь, фасад, вода и слив
K-07	TAKI 49-U/IF	490×440×200	800	вырез по типу монтажа и образцу

2. Остров и проходы

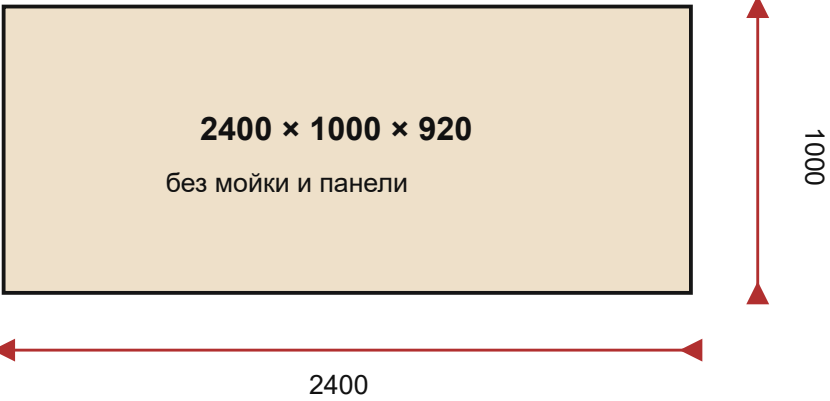

Проход до линии: 1100–1200 — проверить на объекте.

Открытая ПММ не должна блокировать основной маршрут.

Стол Авалон в разложенном виде: 2000×800.

4. Верхняя линия / вода / воздух

K-05 Domina 60 598×290×182 · канал D150	K-06 JBMO725BK01 595×317×390
K-08 NARA-S LG H242 · вылет 186 · отверстие D35 рычаг не упирается в фартук	K-09 NAGARE 500 D205×H370 под мойкой розетка + слив + доступ

До заказа: получить PDF-инструкции всех приборов, чистовой обмер, схему ЭОМ/БК/ОВ и подписи трёх специалистов.


Статус листа: координация, не рабочая документация.

Дима — благоустройство Дом и участок, Ставрополь	Стадия ЭП	Лист КМ-04
Кухня. Товары и ниши	Масштаб граф.	30.07.2026
Эскиз / координация		v21


AP-05. План расстановки мебели — спальни 2 этажа

Паспортные габариты мебели из реестра v21. Координаты переносятся в Cinema 4D v20.2. Размеры в мм.


1. Спальня родителей — 4430 × 3640

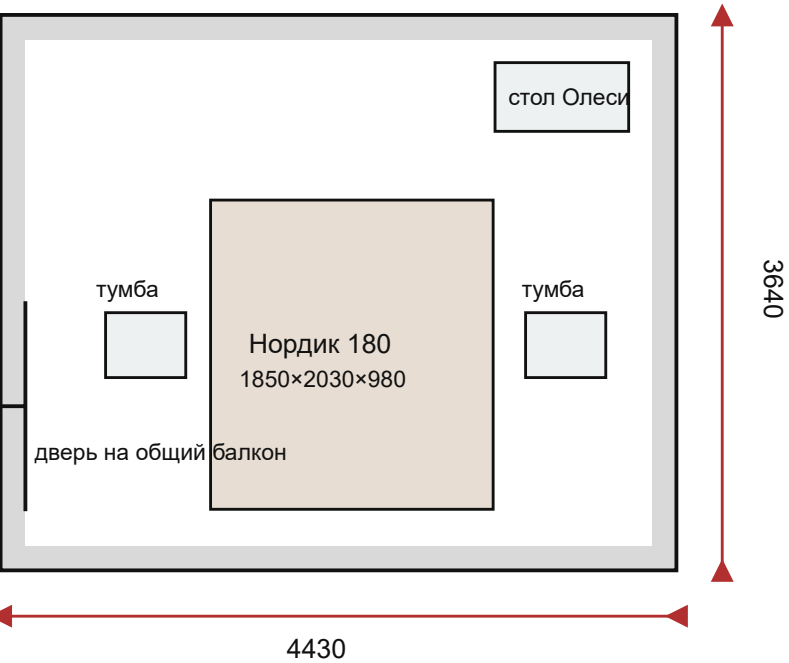

2. Детская Дарины — 4450 × 3950

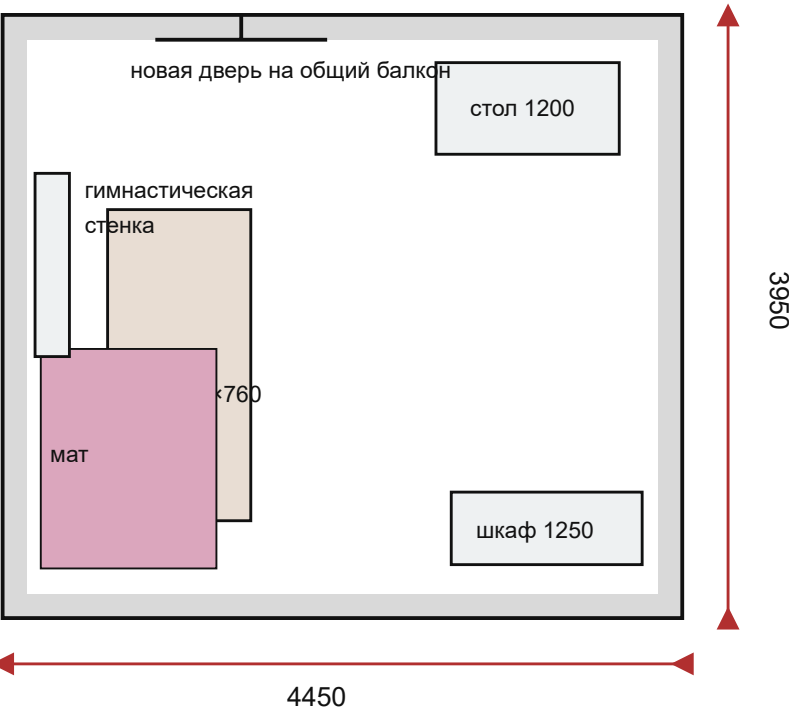

3. Детская Ярика — 5430 × 3950

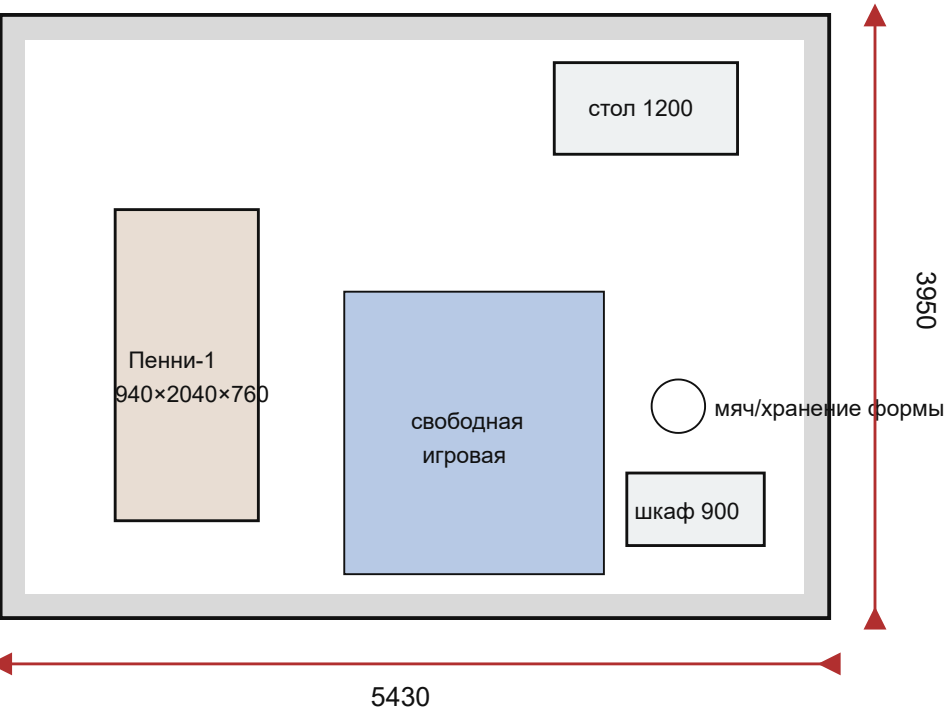

Условные обозначения и правила монтажа

- 1. Контрольные проходы между мебелью и стенами измерить после чистовой отделки.
- 2. Розетки, бра и выключатели привязывать от осей конкретной мебели, а не «примерно по стене».
- 3. Новую дверь детской на балкон выполнить только после расчёта усиления проёма и узла гидроизоляции.
- 4. Высокие детские экраны и ограждение общего балкона — отдельный конструктивный лист.
- 5. Кровати и столы — по паспортам К/Ф-04...F-08; шкафы — только после чистового обмера.


СПДС-ориентир: ГОСТ Р 21.101-2020 и ГОСТ 21.501-2018. Статус: координация, не рабочая документация.

Связанные рендеры Cinema 4D: CAM_14/CAM_41 — родители; CAM_15/CAM_42 — Дарина; CAM_16/CAM_43 — Ярик.
Связанный файл модели: Дима_Облагораживание_Master_v20_2.c4d
Основание геометрии: PDF, лист 8 + изменения заказчика по общему балкону.

Дима — благоустройство Дом и участок, Ставрополь	Стадия ЭП	Лист AP-05
План мебели. Спальни	Масштаб граф.	30.07.2026
Эскиз / координация		v21

AP-05.1. Спальня родителей — план расстановки

Размеры в мм · вид сверху · север/сторона балкона слева · координационная стадия ЭП

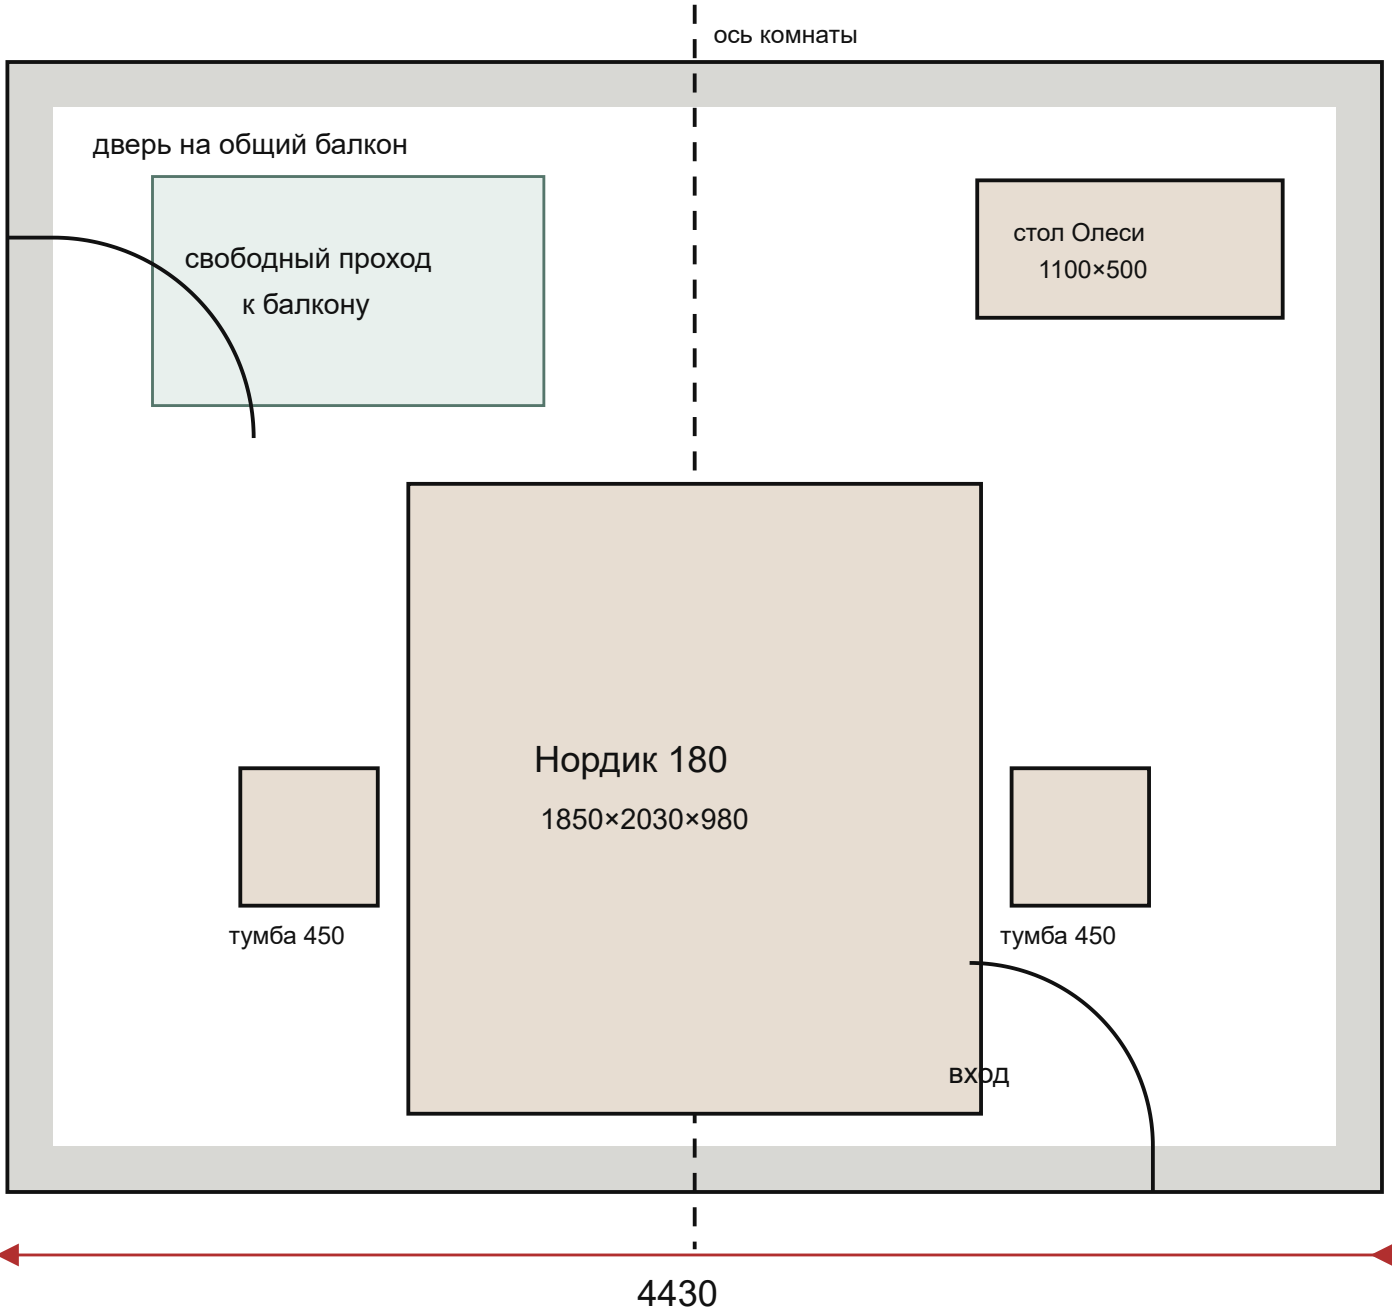

Привязки для мебели

- Нордик 180: 2030×1850×980, по центральной оси.
- Тумбы: симметрично относительно изголовья.
- Проход к балконной двери не занимать.
- Стол Олеси — по стене Б, не перед проёмом.

Что проверить на объекте

1. Чистовые 4430×3640 и диагонали.
2. Реальные проёмы, наличники и радиаторы.
3. Траекторию створки балконной двери.
4. Розетки — от фактического изголовья Нордик 180.

Связанные C4D-камеры: CAM_14, CAM_41

Развёртки стен: лист AP-06


Основание: PDF лист 8 + изменения заказчика

Дима — благоустройство · Ставрополь	Стадия ЭП	AP-05.1
Спальня родителей. План	Масштаб граф.	v21
Эскиз/координация — не рабочая документация		

AP-06. Спальня родителей — развёртки четырёх стен


Кровать Нордик 180: 2030×1850×980 мм. Чистая высота модели 2900. Выводы уточнить после обмера.

А. Стена изголовья, L=4430

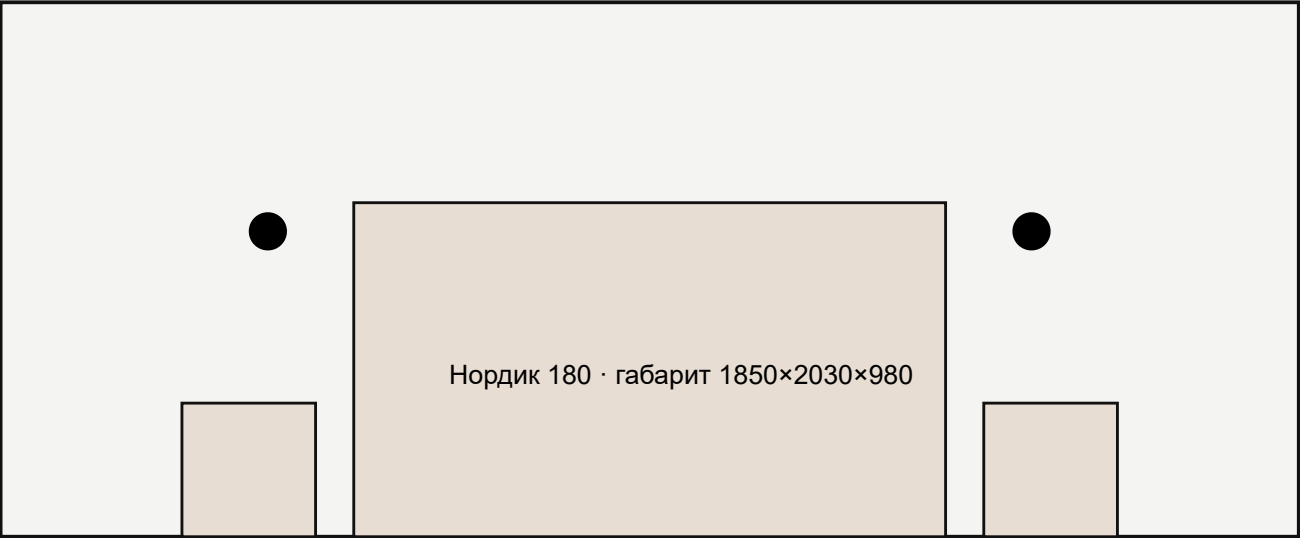


бра по осям тумб, розетки/USB + выключатели у кровати


Б. Стена входа, L=4430

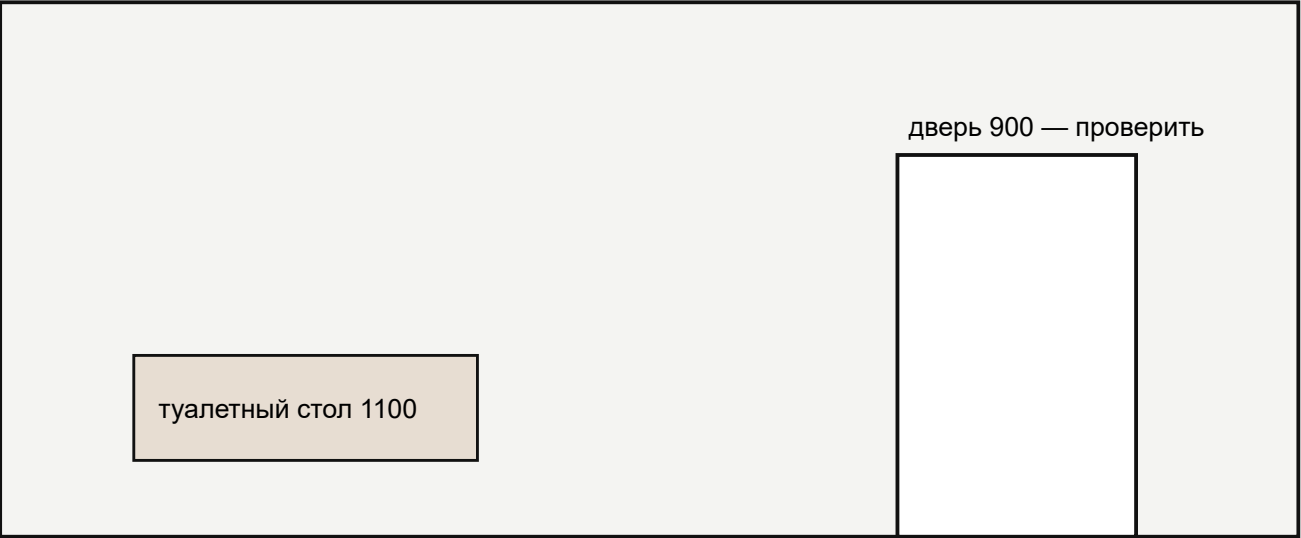

В. Левая стена, L=3640

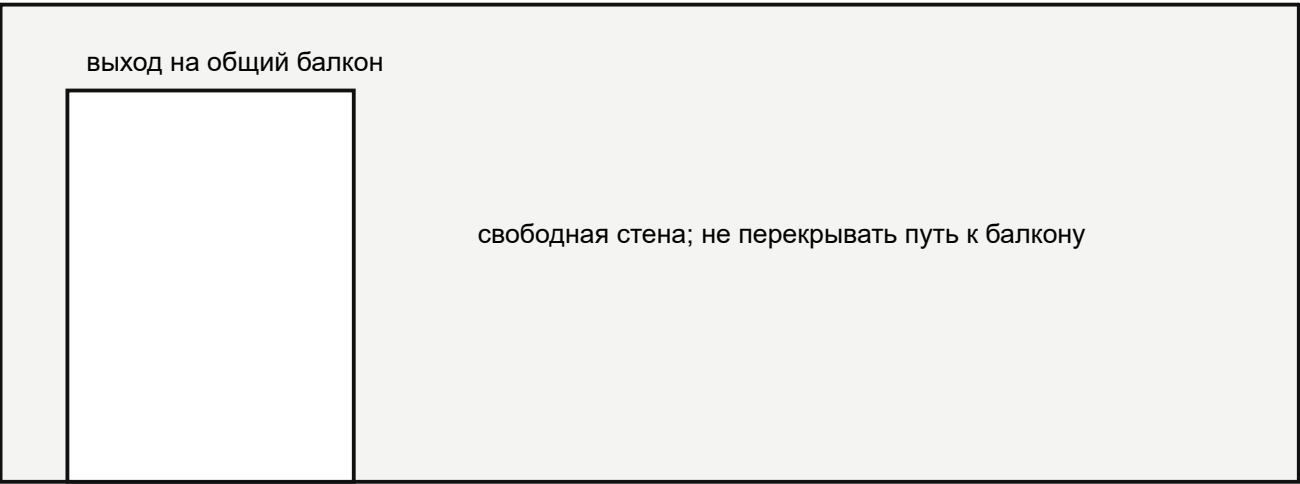

Г. Правая стена, L=3640

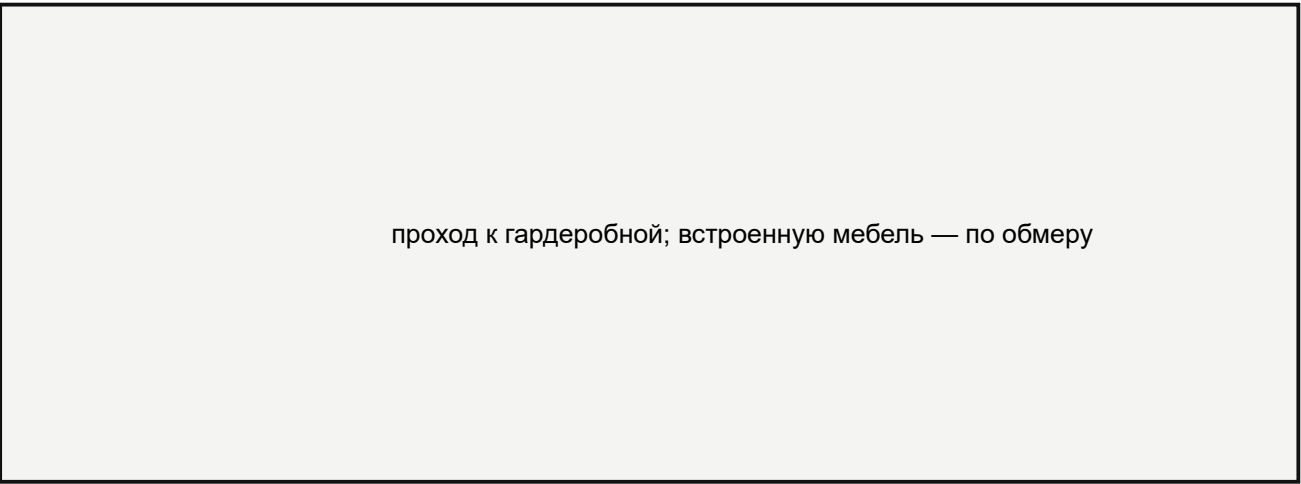


Рендеры рядом на сайте: CAM_14 и CAM_41. Перед мебельным производством снять чистовые размеры и проверить траектории дверей.
СПДС-ориентир: ГОСТ Р 21.101-2020, ГОСТ 21.501-2018. Статус: эскиз/координация.

Дима — благоустройство	Стадия ЭП	AP-06
Спальня родителей	Масштаб граф.	v21
Развёртки стен		

AP-05.2. Детская Дарины — план расстановки

Размеры в мм · вид сверху · новая дверь на общий балкон показана как изменение заказчика

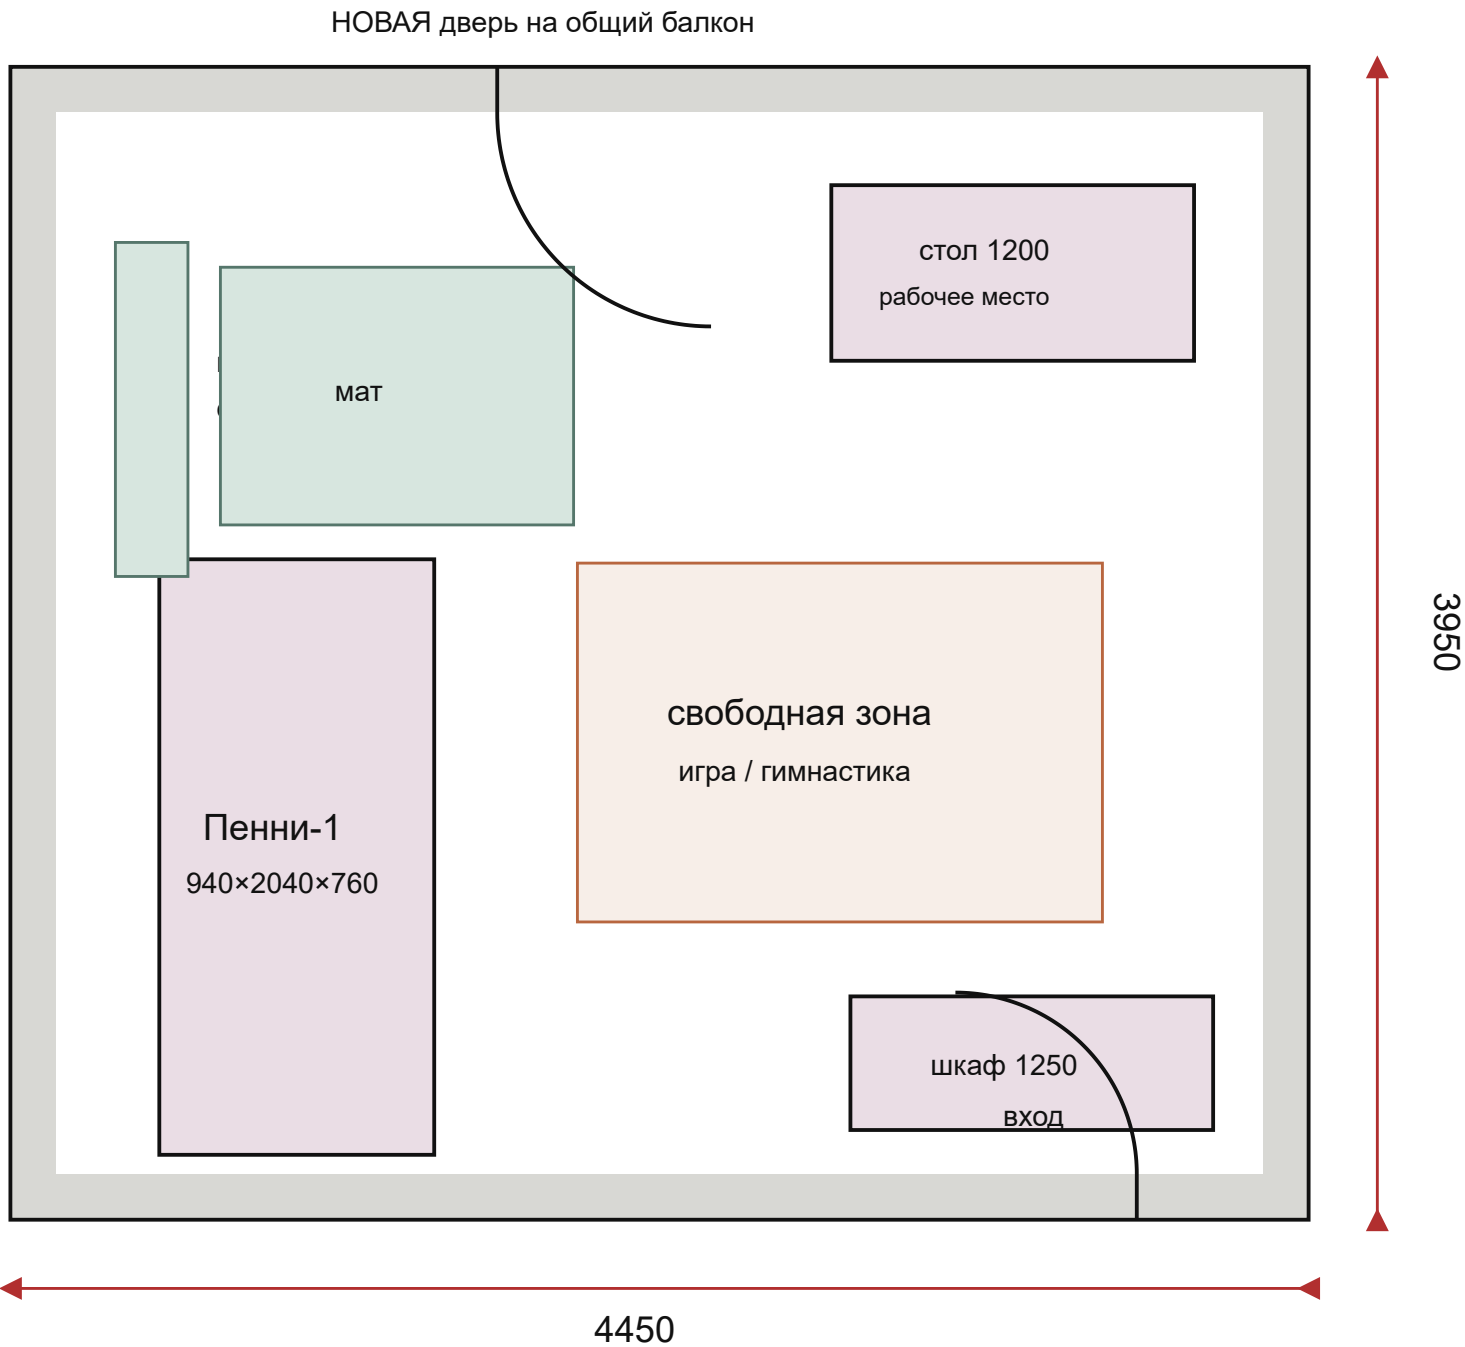

Привязки для мебелировщика

- Пенни-1: 2040×940×760 — вдоль левой стены.
- Стол Милна: 1200×600×750 — возле естественного света.
- Шкаф 1250 — у входной стены.
- Центр комнаты сохраняется свободным.

Обязательные проверки

1. Новый проём — расчёт конструктора до работ.
2. Узлы порога, гидроизоляции и примыкания.
3. Детское ограждение балкона без лазания.
4. Крепёж спортстенки — по материалу стены.
5. Розетки не размещать в зоне спортснаряда.

Связанные C4D-камеры: CAM_15, CAM_42

Развёртки стен: лист AP-07


Основание: PDF лист 8 + изменение заказчика

Дима — благоустройство · Ставрополь	Стадия ЭП	AP-05.2
Детская Дарины. План	Масштаб граф.	v21
Эскиз/координация — не рабочая документация		

AP-07. Детская Дарины — развёртки четырёх стен


Комната 4450 × 3950. Новая балконная дверь — изменение заказчика, только после конструктивного расчёта.

А. Фасадная стена, L=4450

 


новая дверь на общий балкон, порог и безопасное стекло по проекту

Б. Стена рабочего места, L=4450

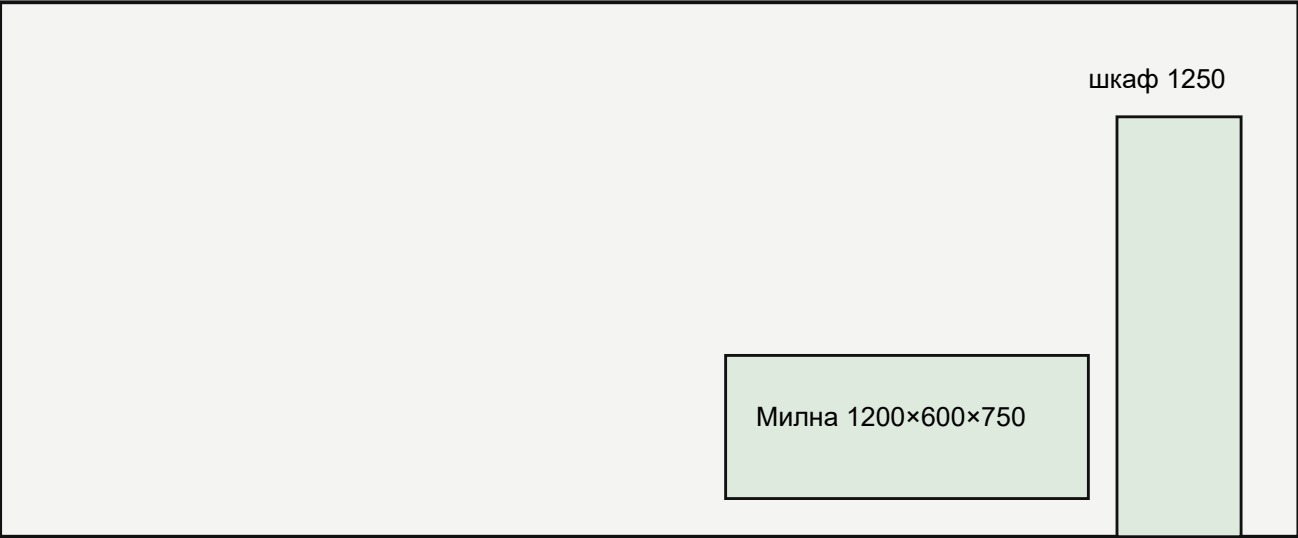


2×230 В + USB/данные над столом; свет слева для правши

В. Спортивная стена, L=3950

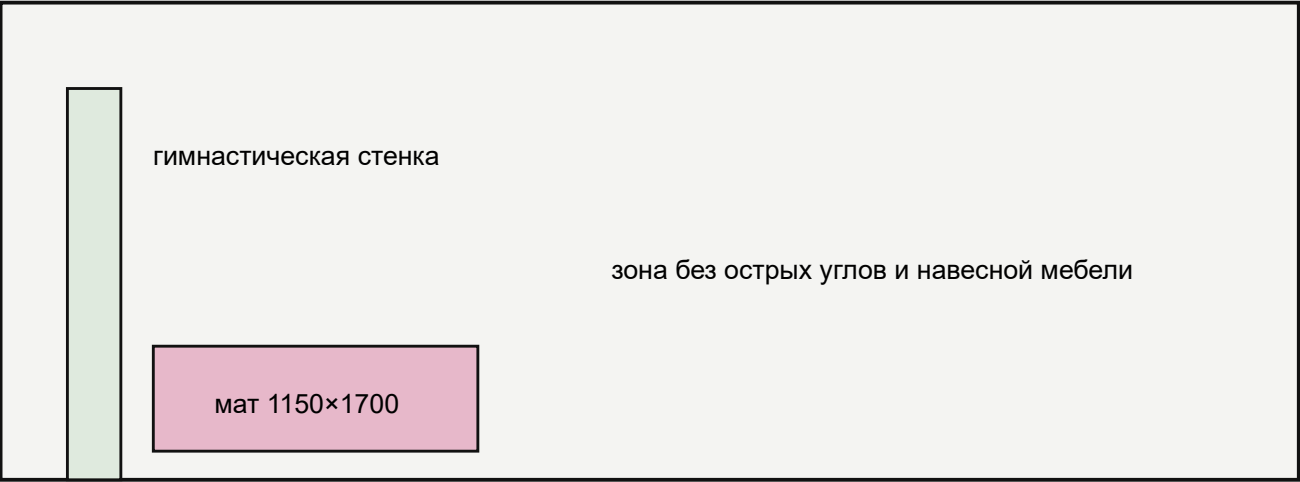

Г. Стена кровати, L=3950

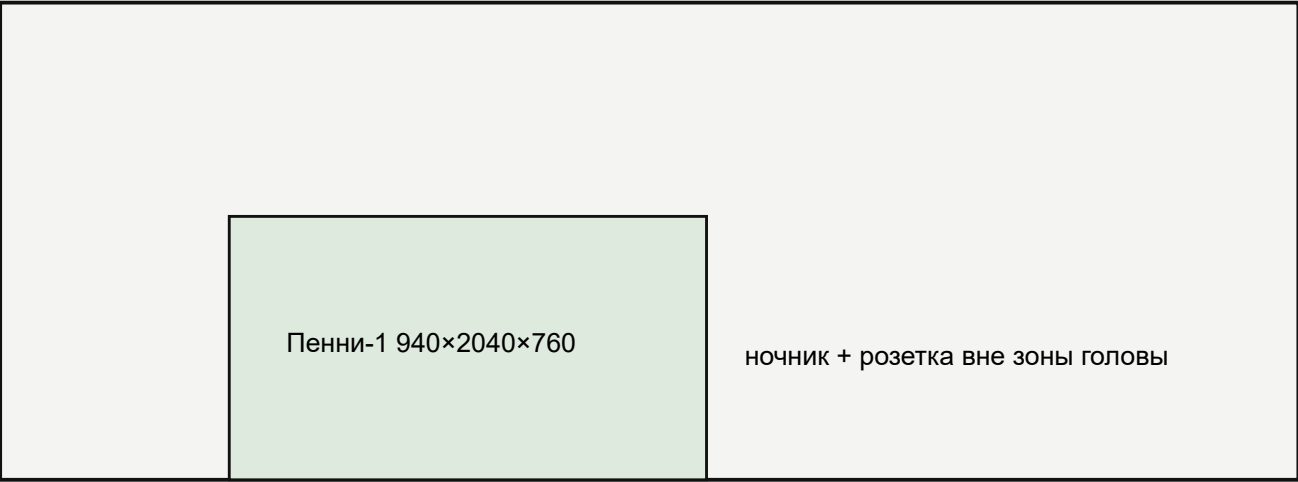


Рендеры рядом на сайте: SAM_15 и SAM_42. Проверить безопасные крепления спортстенки и ограждение балкона.
СПДС-ориентир: ГОСТ Р 21.101-2020, ГОСТ 21.501-2018. Статус: эскиз/координация.

Дима — благоустройство	Стадия ЭП	AP-07
Детская Дарины	Масштаб граф.	v21
Развёртки стен		

AP-05.3. Детская Ярика — план расстановки

Размеры в мм · вид сверху · хранение спортивной формы отделено от свободной игровой зоны

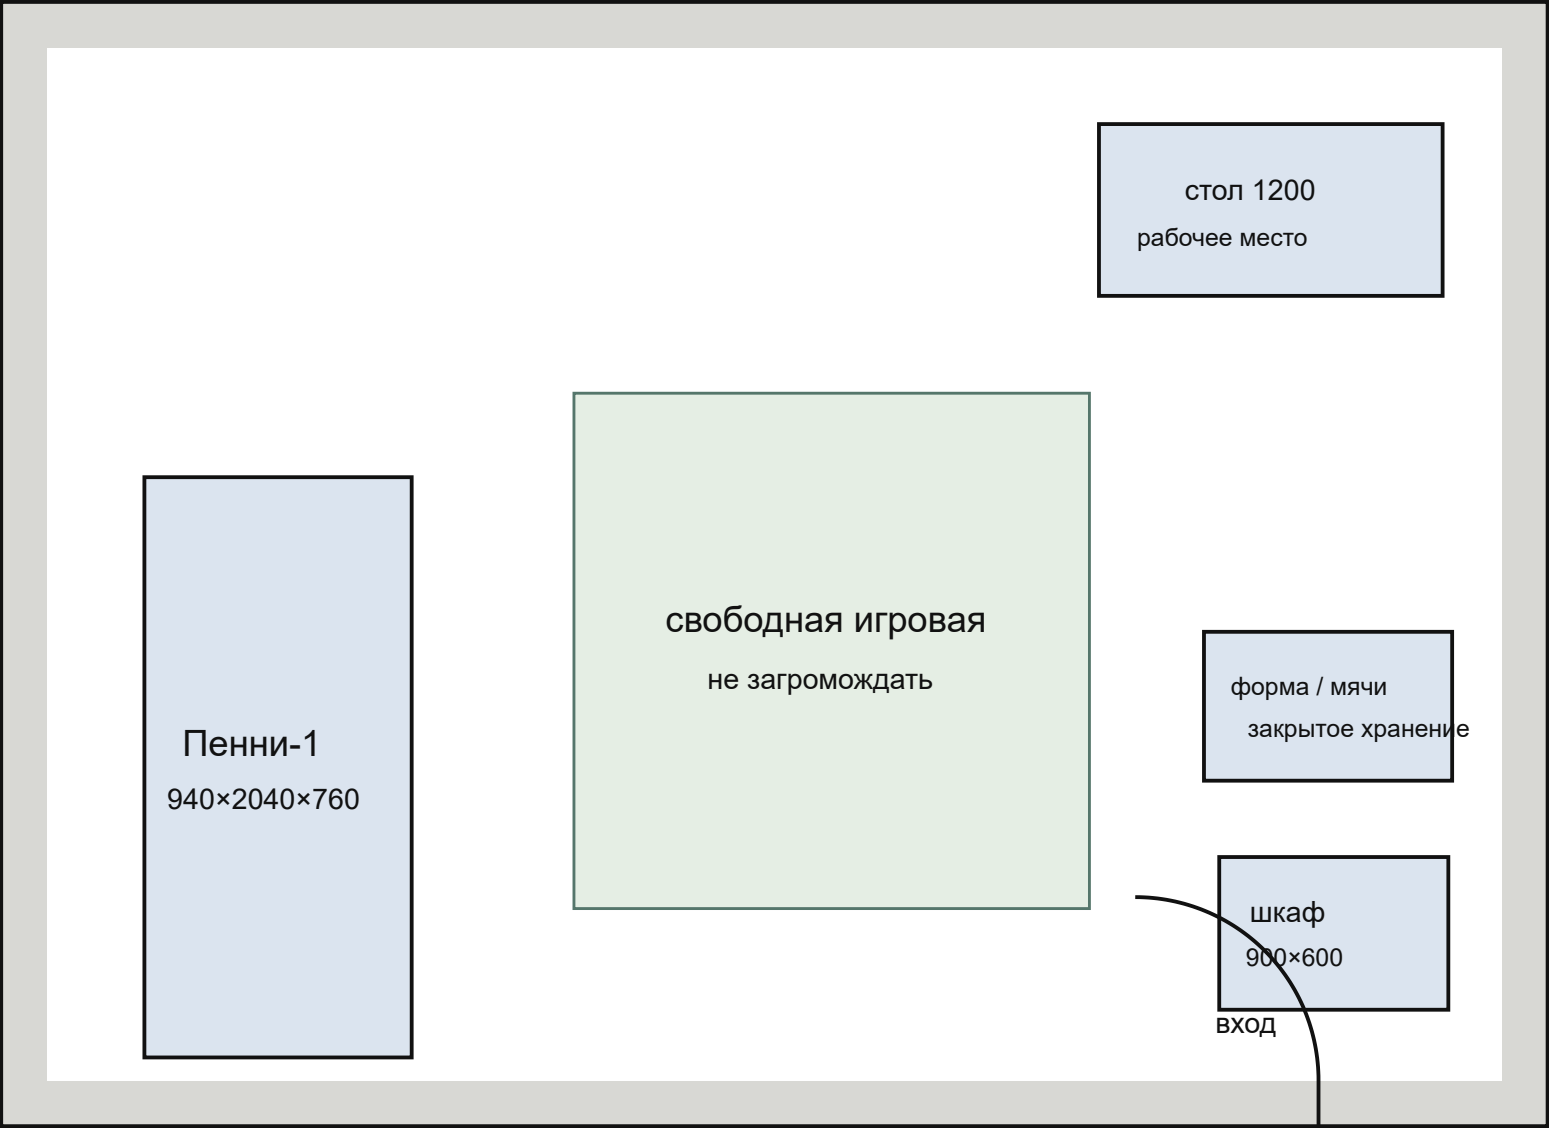

Привязки для мебелировщика

- Пенни-1: 2040×940×760 — вдоль левой стены.
- Стол Дикинс: 1200×600×760 — у естественного света.
- Шкаф 900 и спортхранение — у входа.
- Центральную игровую зону не занимать.

Что проверить на объекте

1. Чистовые 5430×3950 и положение окна.
2. Дверную створку и путь эвакуации.
3. Розетки стола и ночной подсветки.
4. Анкерование высокой мебели к стене.

Связанные C4D-камеры: CAM_16, CAM_43

Развёртки стен: лист AP-08


Основание: PDF лист 8

Дима — благоустройство · Ставрополь Стадия ЭП	AP-05.3
Детская Ярика. План	Масштаб граф. v21
Эскиз/координация — не рабочая документация	


AP-08. Детская Ярика — развёртки четырёх стен

Комната 5430 × 3950. Центральная игровая зона сохраняется свободной.

А. Фасадная стена, L=5430

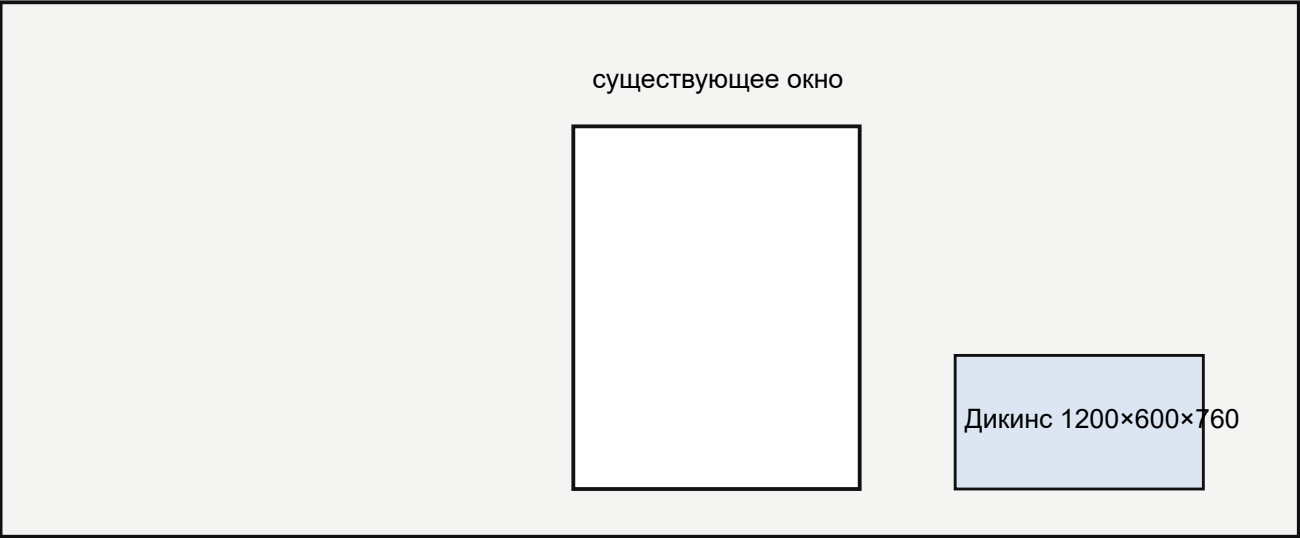


Б. Стена хранения, L=5430

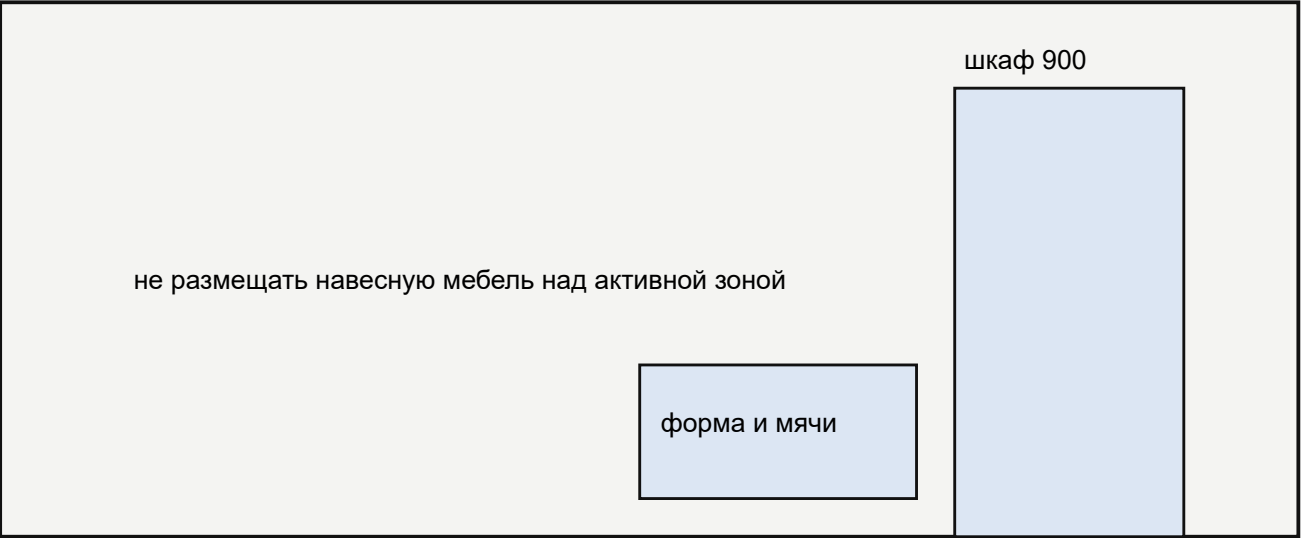

В. Стена кровати, L=3950



Г. Стена входа, L=3950

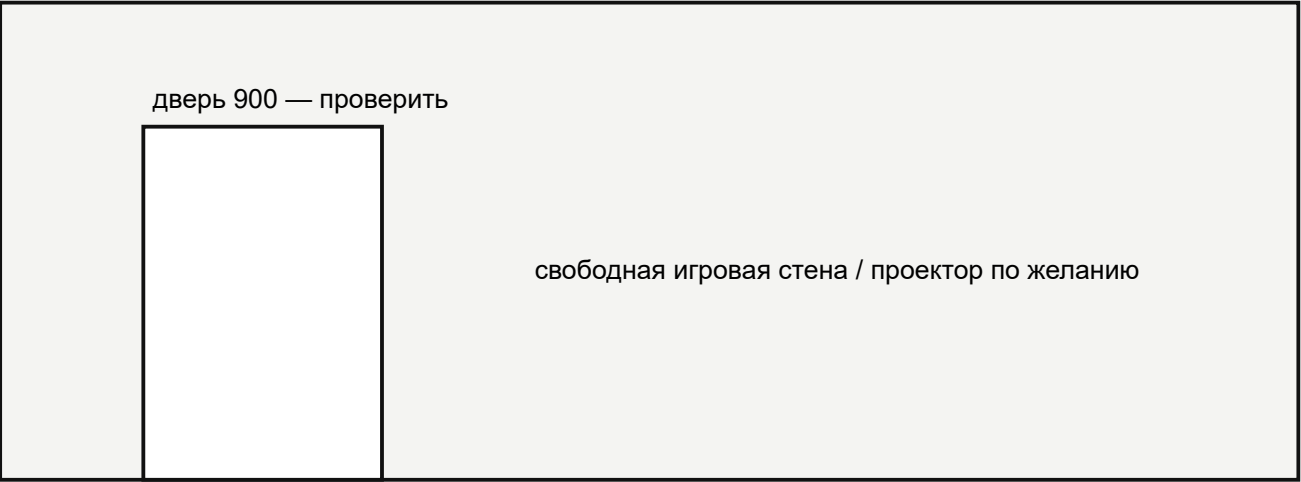

Рендеры рядом на сайте: CAM_16 и CAM_43. До заказа мебели проверить открывание двери и фактический подоконник.
Основание: PDF лист 8; все чистовые размеры подтвердить обмером. СПДС-ориентир: ГОСТ Р 21.101-2020. Статус: эскиз/координация.


Дима — благоустройство	Стадия ЭП	AP-08
Детская Ярика	Масштаб граф.	v21
Развёртки стен		

AP-09 · Мангальная по фото и плану первого этажа


Координационный лист · внешний задний правый угол террасы · размеры в мм · мойка встроена в столешницу

ПЛАН · L-образная зона 1640 × 1990

Верх листа — внешний край террасы; низ листа — направление к дому

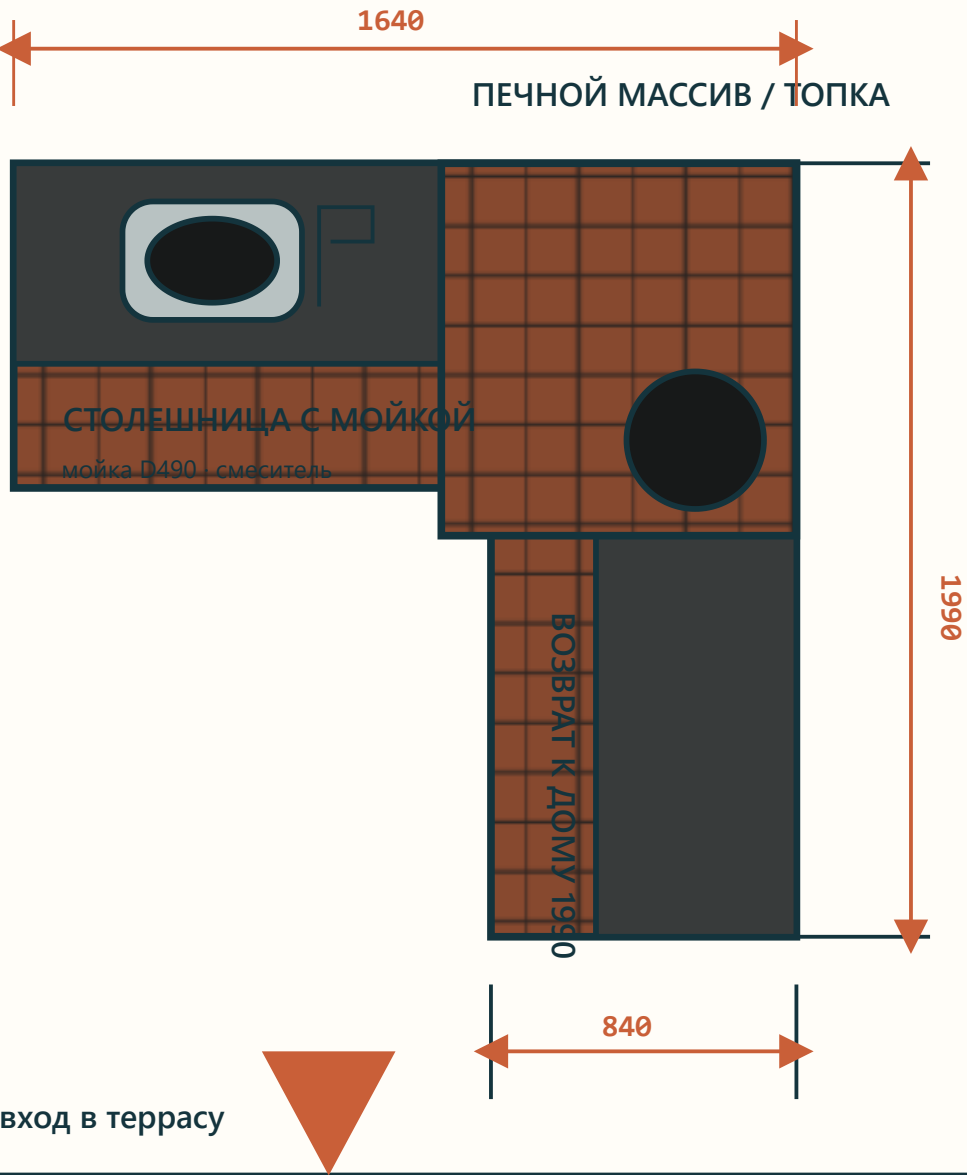

ВИД ИЗНУТРИ ТЕРРАСЫ · как на фото заказчика

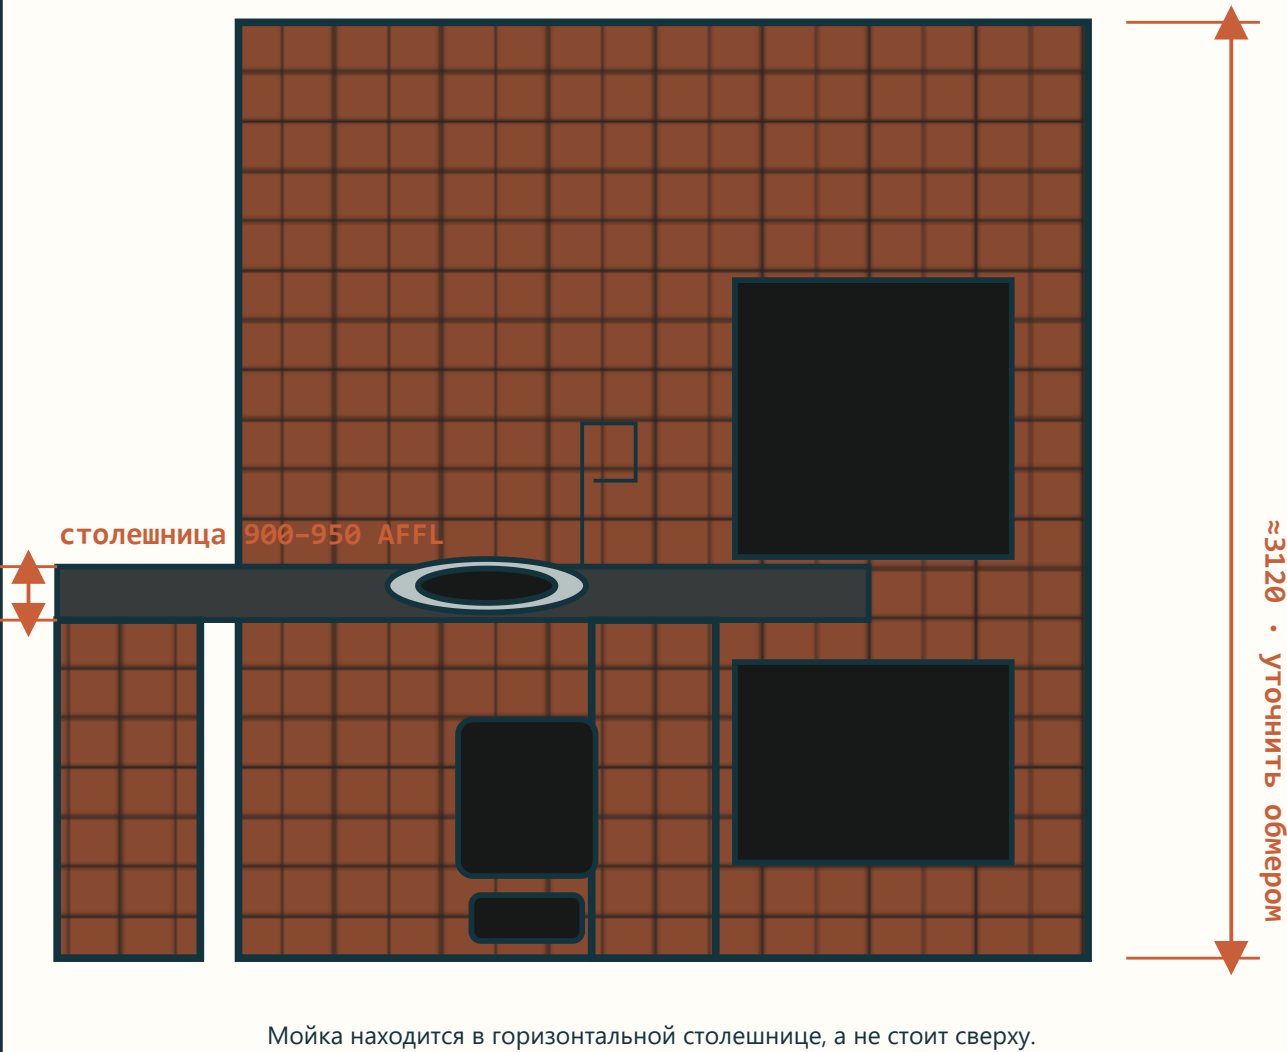

Обязательные проверки до строительства


- Обмерить существующую кладку, высоту плиты террасы и все привязки.
- Печник рассчитывает топку, дымоход, разделки, основание и пожарные отступы.
- БК подтверждает мойку, ХВС/ГВС/слив и зимнее отключение; окна дома не перекрывать.

Проект	Лист	Статус
ДИМА · БЛАГОУСТРОЙСТВО	AP-09	ЭСКИЗ v20.2 31.07.2026





К-01. Котельная — координационная модель Cinema 4D v20.1

Единицы: мм · помещение на листе 7 PDF: 8,24 м² · модельная граница: 2450 × 2950 · окончательные чистовые размеры — после обмера

План, вид сверху

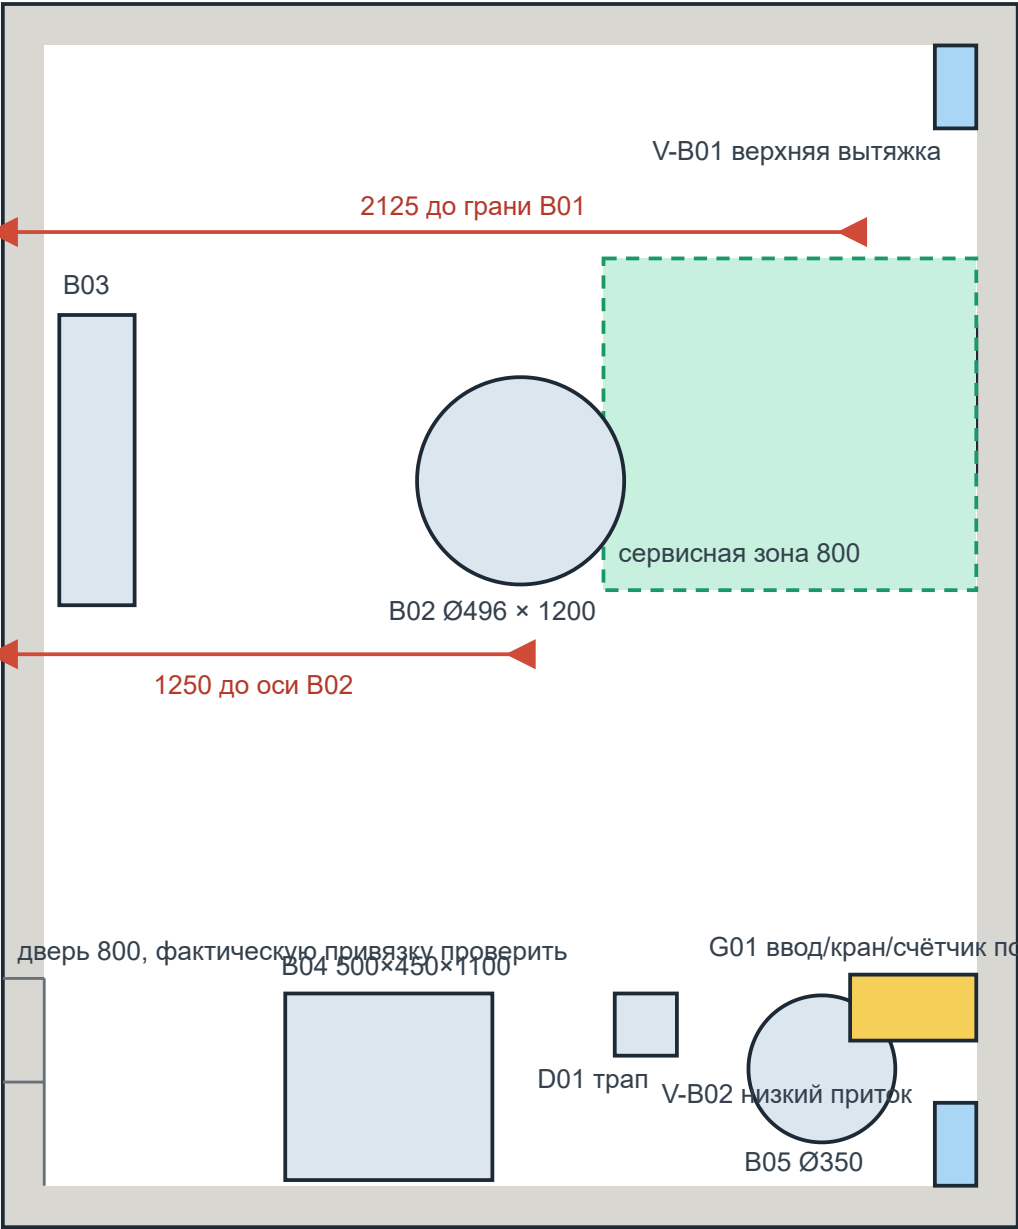

Развёртки стен — те же координаты C4D

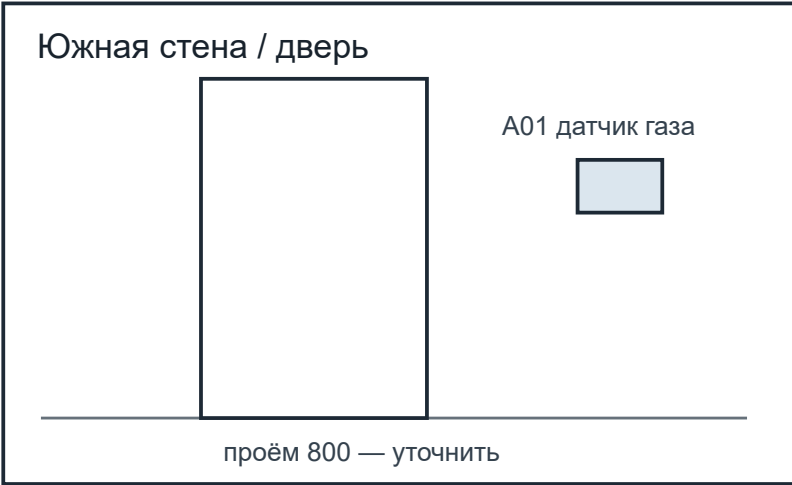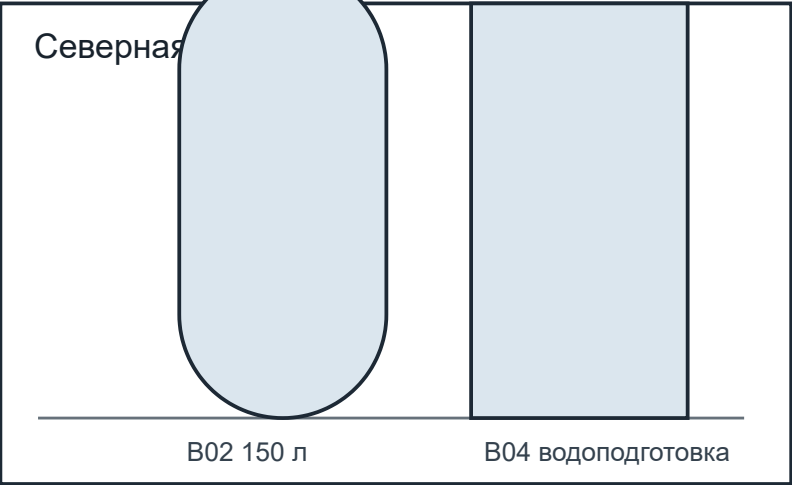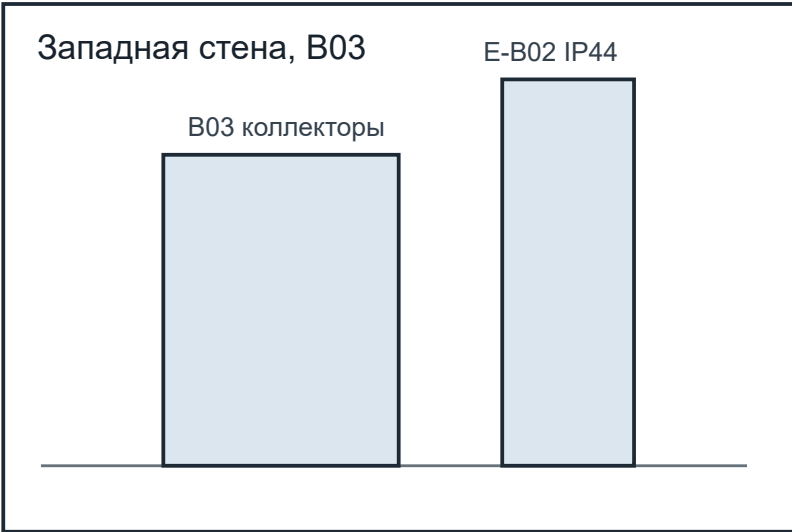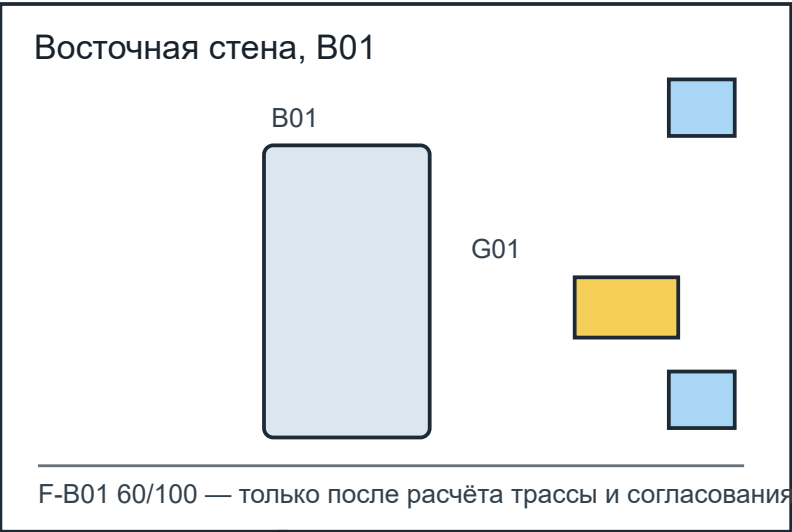

До передачи монтажнику обязательно получить

- 1. Технические условия на газ. 2. Теплотери и выбранную мощность. 3. Паспорт котла и схему дымоудаления.
- 4. Обмер помещения, окна/двери/высоту. 5. Расчёт воздухообмена. 6. Анализ воды. 7. Проект лицензированной организации.

[B01 — официальная карточка BAXI ECO Nova 2025 1.24 F](#)

[B02 — официальная карточка ROMMER 150 л](#)

Статус листа: КООРДИНАЦИЯ / ТЗ. Не рабочий проект газоснабжения и не разрешение на монтаж.

ОВ-01

Котельная. План и развёртки · источник графики: связанный координационный лист

СТАТУС


Эскиз/координация. Размеры подтвердить обмером и профильным расчётом.

ВЫПУСК

v20.2
30.07.2026

В-01. Вентиляция дома — схема и коды объектов Cinema 4D v20.1

Синие линии — приток · красные — общеобменная вытяжка · жёлтые — отдельные системы · сечения и расходы назначает инженер после расчёта

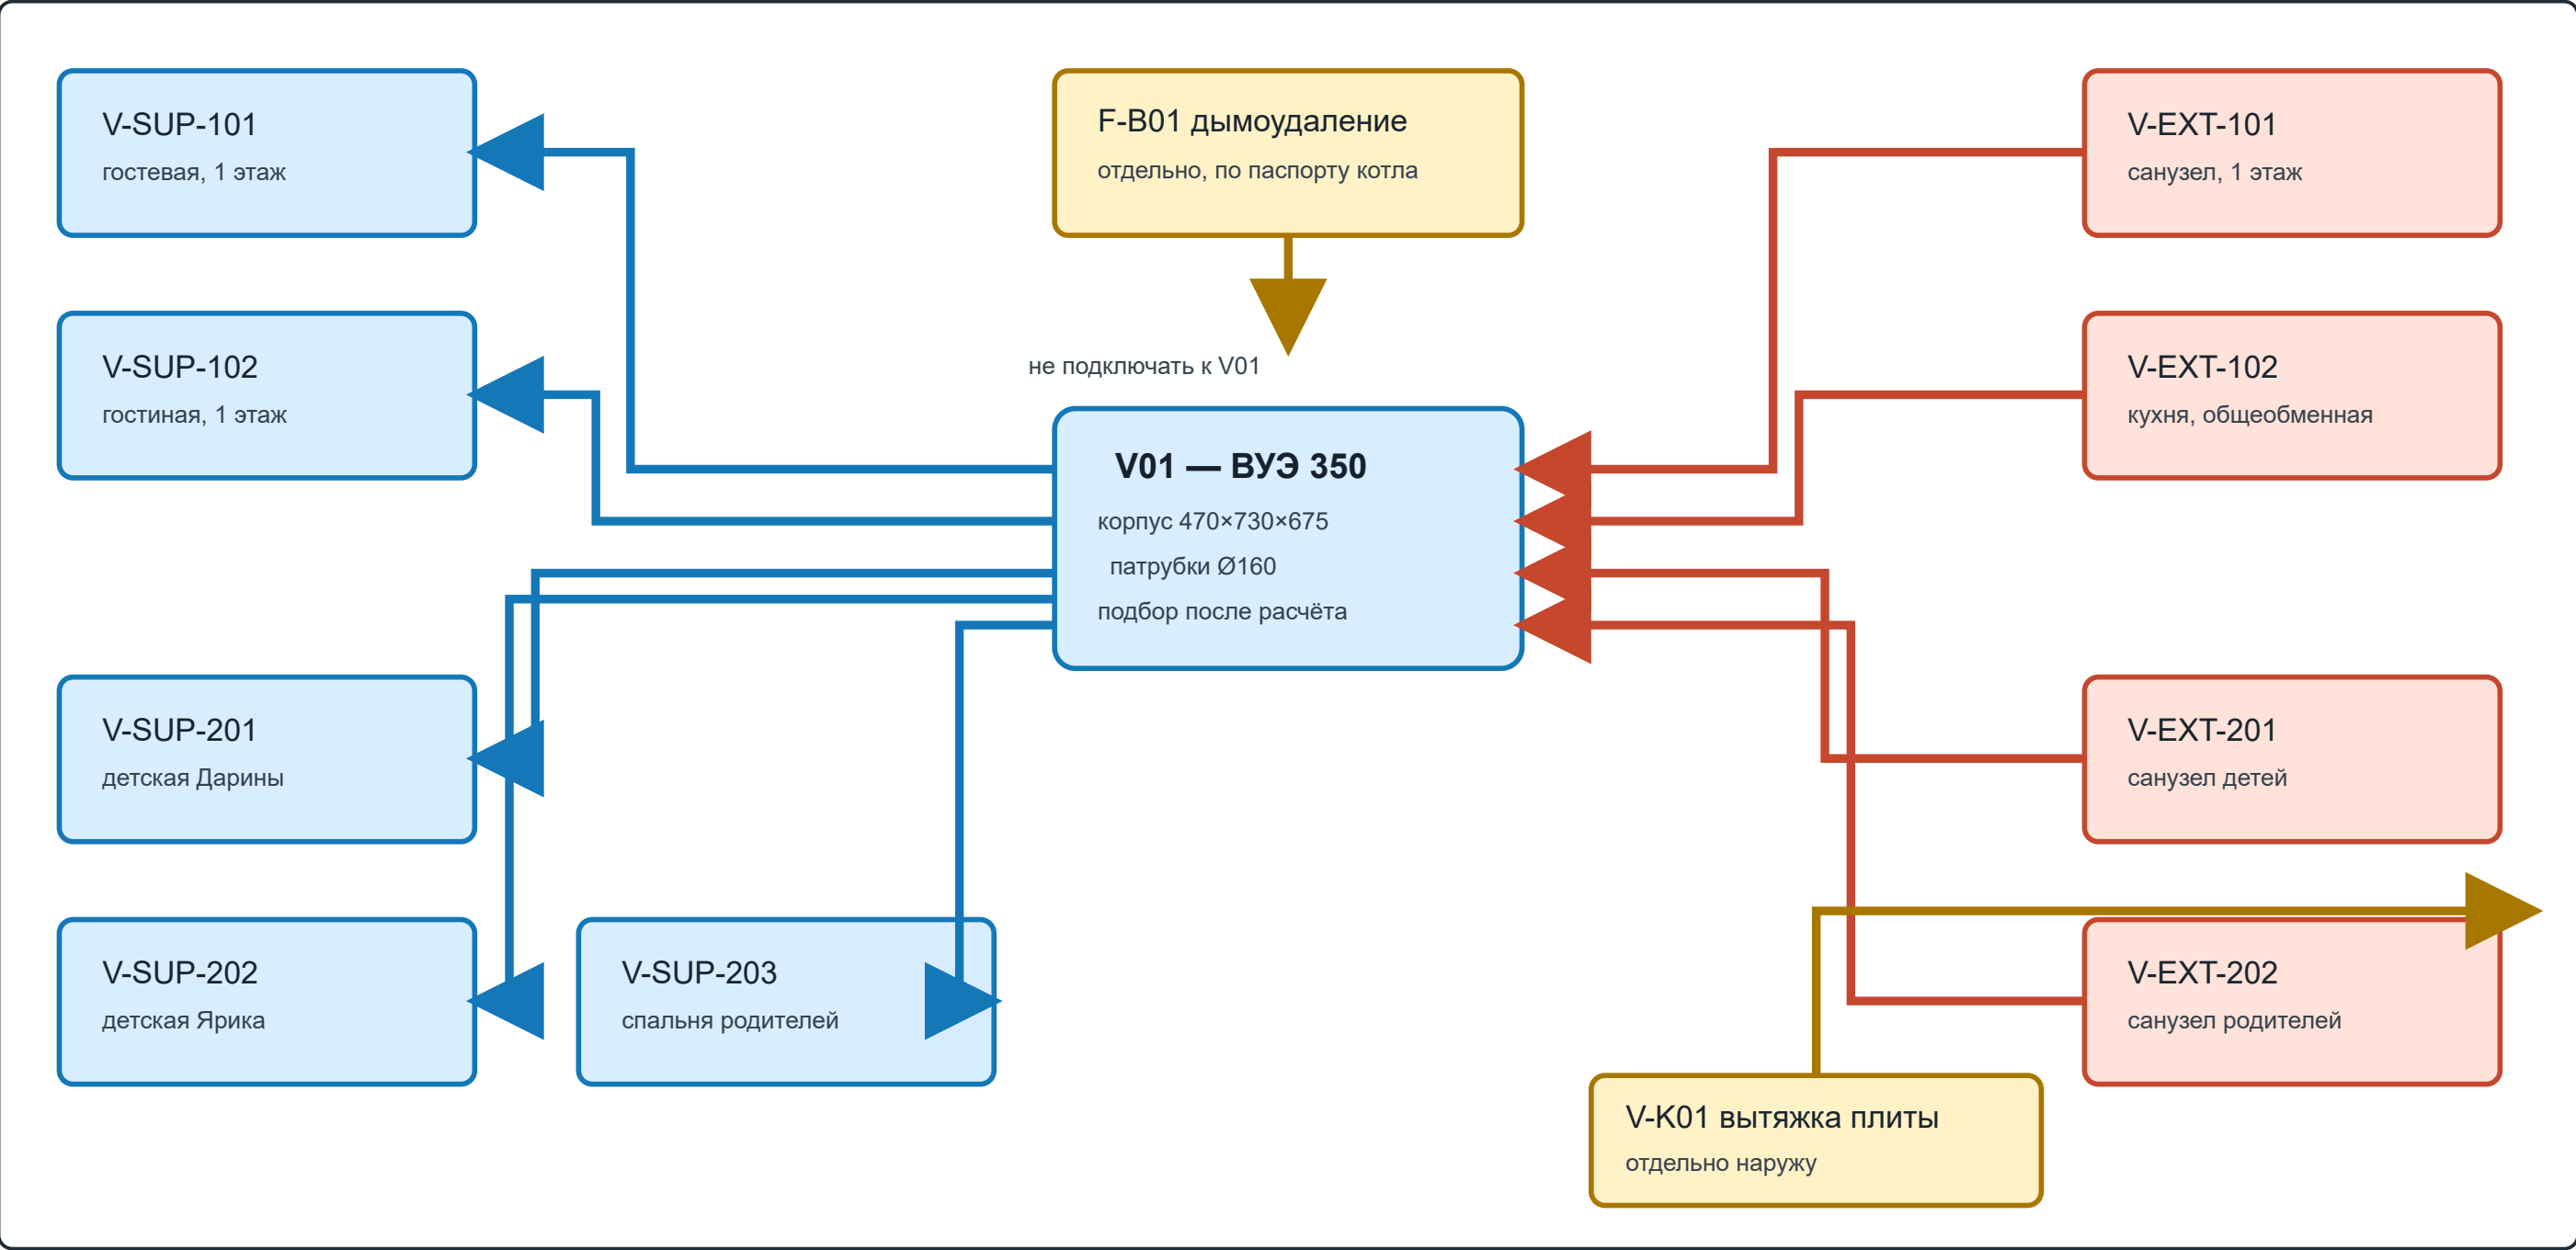

Перед монтажом: обмер → воздухообмен по комнатам → аэродинамика → акустика → противообмерзание → рабочие узлы проходок

[V01 — официальная карточка и CAD-модель ВЕНТС ВУЭ 350 В1Б ЕС А21](#)

ОВ-02

Вентиляция. Принципиальная схема · источник графики: связанный координационный лист

СТАТУС


Эскиз/координация. Размеры подтвердить обмером и профильным расчётом.

ВЫПУСК

v20.2
30.07.2026

ЛД-20.01 · Посадочный план — участок 20 × 30 м

Ставрополь · меньше деревьев, больше цветов и кустарников · координаты X/Y от переднего левого угла участка · концепция до анализа почвы, солнца и полива

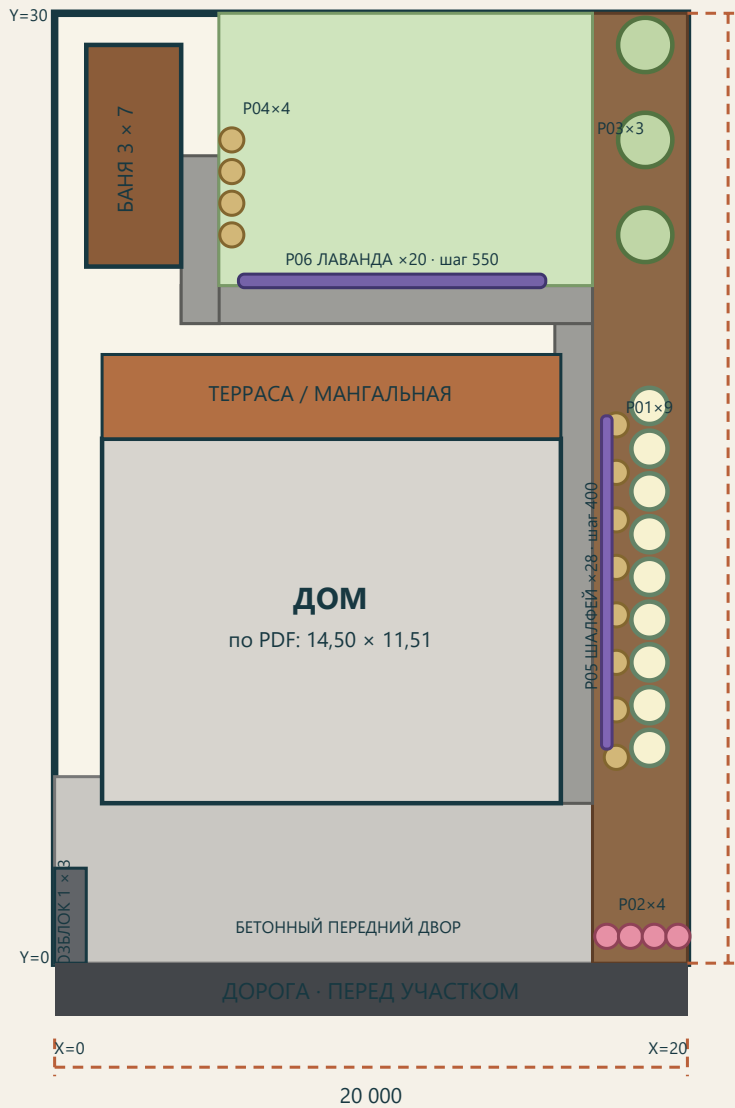

Спецификация и точные правила посадки

Код	Наименование	Количество	Координаты (X, Y)	Высота	Ширина	Дополнительные требования
P01	Гортензия метельчатая Bobo <i>Hydrangea paniculata 'Bobo'</i>	9	X=18,80; Y=6,80...17,60 9 центров, ряд вдоль дома	1,35 м	0,9×1,2 м	1,80 м от дорожки; 1,20 м от забора цветущий фон, окно/свет не закрывать
P02	Спирея японская Little Princess <i>Spiraea japonica 'Little Princess'</i>	4	Y=0,85; X=17,45/18,20/18,95/19,70 низкий передний ряд	0,75 м	0,5–0,9×0,6–1,0	0,85 м от дороги; стричь единым бордюром сохранять обзор при выезде автомобиля
P03	Дёрен Sibirica Variegata <i>Cornus alba 'Sibirica Variegata'</i>	3	X=18,67; Y=23,0/26,0/29,0 задний экран	3,00 м	1,5–2,5×1,5–2,5	≥ 1,3 м от забора и дорожки формировать обрезкой; проверить сеть/дренаж
P04	Вейник Karl Foerster <i>Calamagrostis × acutiflora 'Karl Foerster'</i>	12	8 шт X=17,75 Y=6,5...17,0 4 шт X=5,60 Y=23...26	1,50/1,00	1,5×0,5 м	центр ≥ 0,75 м от края дорожки вертикальный ритм, не закрывает обзор
P05	Шалфей дубравный, фиолетовый сорт <i>Salvia nemorosa cv.</i>	28	X=17,30; Y=6,6...17,4 передний ярус правой полосы	0,40 м	0,5–0,8×0,4	центр 0,30 м от покрытия мульча; срезать соцветия для повтора
P06	Лаванда узколистная Hidcote <i>Lavandula angustifolia 'Hidcote'</i>	20	Y=21,75; X=5,80...16,25 край задней дорожки	0,55 м	0,35–0,6×0,75	центр 0,35 м от покрытия; полный дренаж солнечная ароматная линия
ИТОГО	0 новых деревьев · 16 кустарников · 60 многолетников/злаков			Сажать блоками, не единичной «коллекцией».		

ТЗ садовнику и контроль результата

- До цены: геодезическая разбивка границ, фото солнца 09:00/13:00/17:00, анализ pH/механического состава, проверка застойной воды.
- Вынести оси X/Y и центры P01–P06 колышками. Заказчик принимает раскладку до копки ям.
- Согласовать сорт, посадочный размер и фото партии. Замены допускаются только с новой взрослой шириной и пересчётом шага.
- Устроить капельный полив отдельными зонами: кустарники / многолетники / лаванда. Лаванду не подключать к переувлажнённой линии.
- После посадки: исполнительная схема фактических центров, фото корневой шейки, акт полива, гарантия приживаемости и календарь ухода.

Визуализация: показывать три состояния — «посадка», «3-й год», «взрослое». Финальные рендеры сайта должны совпадать с кодами P01–P06.

Сортовой подбор подтвердить местным агрономом после осмотра. Источники размеров: RHS; локальную доступность и качество партии проверять у питомника перед оплатой.

Проверочные источники: rhs.org.uk — Bobo, Little Princess, Cornus, Salvia, Hidcote; наличие в Ставрополе сверять перед закупкой. Дата концепции: 30.07.2026.

ГП-01

Посадочный план · источник графики: связанный координационный лист

СТАТУС

Эскиз/координация. Размеры подтвердить обмером и профильным расчётом.

ВЫПУСК

v20.2
30.07.2026