

КООРДИНАЦИОННЫЙ КОМПЛЕКТ Н1

Дом и участок Дмитрия · Ставрополь · ревизия 00

СТАТУС: СПДС-ОРИЕНТИРОВАННАЯ КООРДИНАЦИЯ, НЕ РАБОЧАЯ ДОКУМЕНТАЦИЯ

Основание: исходный архитектурный PDF + зафиксированные требования заказчика Н1.

ВЕДОМОСТЬ ЛИСТОВ

01 Н1-00	Общие данные и ведомость листов	КООРДИНАЦИЯ
02 Н1-ГП-01	Схема участка и контроль размещения	КООРДИНАЦИЯ
03 Н1-АР-01	Исходная схема посадки дома	ИСХОДНЫЙ ЛИСТ
04 Н1-АР-02	План первого этажа	ИСХОДНЫЙ ЛИСТ
05 Н1-АР-03	План второго этажа	ИСХОДНЫЙ ЛИСТ
06 Н1-АР-04	Фасад спереди	ИСХОДНЫЙ ЛИСТ
07 Н1-АР-05	Разрез 1–1 и отметки	ИСХОДНЫЙ ЛИСТ
08 Н1-АР-06	Общий балкон над гаражом — схема изменения	ТРЕБУЕТ КОНСТРУКТОРА
09 Н1-БН-01	Баня 7000 × 3000 — планировочная координация	ТРЕБУЕТ ПРОЕКТА БАНИ
10 Н1-ТХ-01	Мангальная зона 1610 × 1970 — план и фасад	ТРЕБУЕТ ПЕЧНИКА/ОВ/ВК

НЕЗАКРЫТЫЕ ВОРОТА: G1 обмеры · G2 конструктив · G3 инженерия · G4 геодезия · G5 CAD · G6 визуальная приёмка · G7 выпуск

Исходный PDF: Снимок экрана 2025—09—13 в 18.38.43.pdf

SHA-256: 2794F112FE36EA85B52B9C7A308E4BC0D823477563BD06D945743EC63A9B2A1E

Михайличенко · Инженер ИИ

Общие данные и ведомость листов

Н1-00 · Н1-KOORD · 1/10 · —

H1-ГП-01 · H1-KOORD · 2/10 · М 1:150

ПОДЛОЖКА ИЗ ИСХОДНОГО PDF. НЕ ИСПОЛНИТЕЛЬНЫЙ ОБМЕР. ГЕОМЕТРИЯ НЕ ПЕРЕРИСОВЫВАЛАСЬ.

Согласовано

Заказчик

Согласовано

Взам. инв. №

Подп. и дата

Инв. № подл.

Схема посадки дома на участке

СОСЕД СЛЕВА

СОСЕД СПРАВА

ПРОЕЗЖАЯ ЧАСТЬ

Посадка согласована с представителем Заказчика

Утверждаю _____ / _____ /

При разработке схемы посадки дома на участке Заказчиком не были предоставлены топосъемка и градостроительные план земельного участка
Данный об участке взят с публичной кадастровой карты Росреестра - <https://pkk.rosreestr.ru>
При посадке дома, по месту, обязательно выполнить геодезические работы и посадить дом согласно геодезических координат

Кадастровый номер участка – 26:12:011903:1397

Категория земель: Земли поселений (земли населенных пунктов)
Для индивидуального жилищного строительства

Земельный участок по адресу: Российская Федерация, Ставропольский край, г. Ставрополь
ул. Владимира Калмыкова

Уточненная площадь участка: 600 кв.м.
Общая площадь застройки – 227,3 м²;
Коэффициент застройки 37%<40% - проходит

Технико-экономические показатели:
Площадь застройки:
- подвал – 70,09 м²;
- 1эт – 112,65 м²;
- гараж – 63,19 м²;
- крыльцо – 10,43 м²;
- терраса – 41,03 м²;
- 2эт – 112,65 м²;
Полезная площадь:
- подвал 58,56 м²;
- 1эт – 92,51 м²;
- гараж – 56,84 м²;
- 2эт – 92,47 м²;

Здание имеет подвал
Этажность – 2 надземных этажа
1 этаж подземный
Высота здания – 8,09м

Ситуационный план

Изм.	Кол.уч.	Лист	№ док.	Подп.	Дата
Г.А.П.		Левшеков С.С.			
Исполнитель		Левшеков С.С.			
Застройщик					
Заказчик					

Архитектурные решения – АР

Схема посадки дома

Стадия

Лист

Листов

АР

4


СК РАВНОВЕСИЕ

Формат А3А


Михайличенко · Инженер ИИ

Исходная схема посадки дома


Н1-АР-01 · Н1-KOORD · 3/10 · по исходному листу

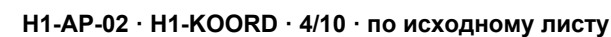

ПОДЛОЖКА ИЗ ИСХОДНОГО PDF. НЕ ИСПОЛНИТЕЛЬНЫЙ ОБМЕР. ГЕОМЕТРИЯ НЕ ПЕРЕРИСОВЫВАЛАСЬ.

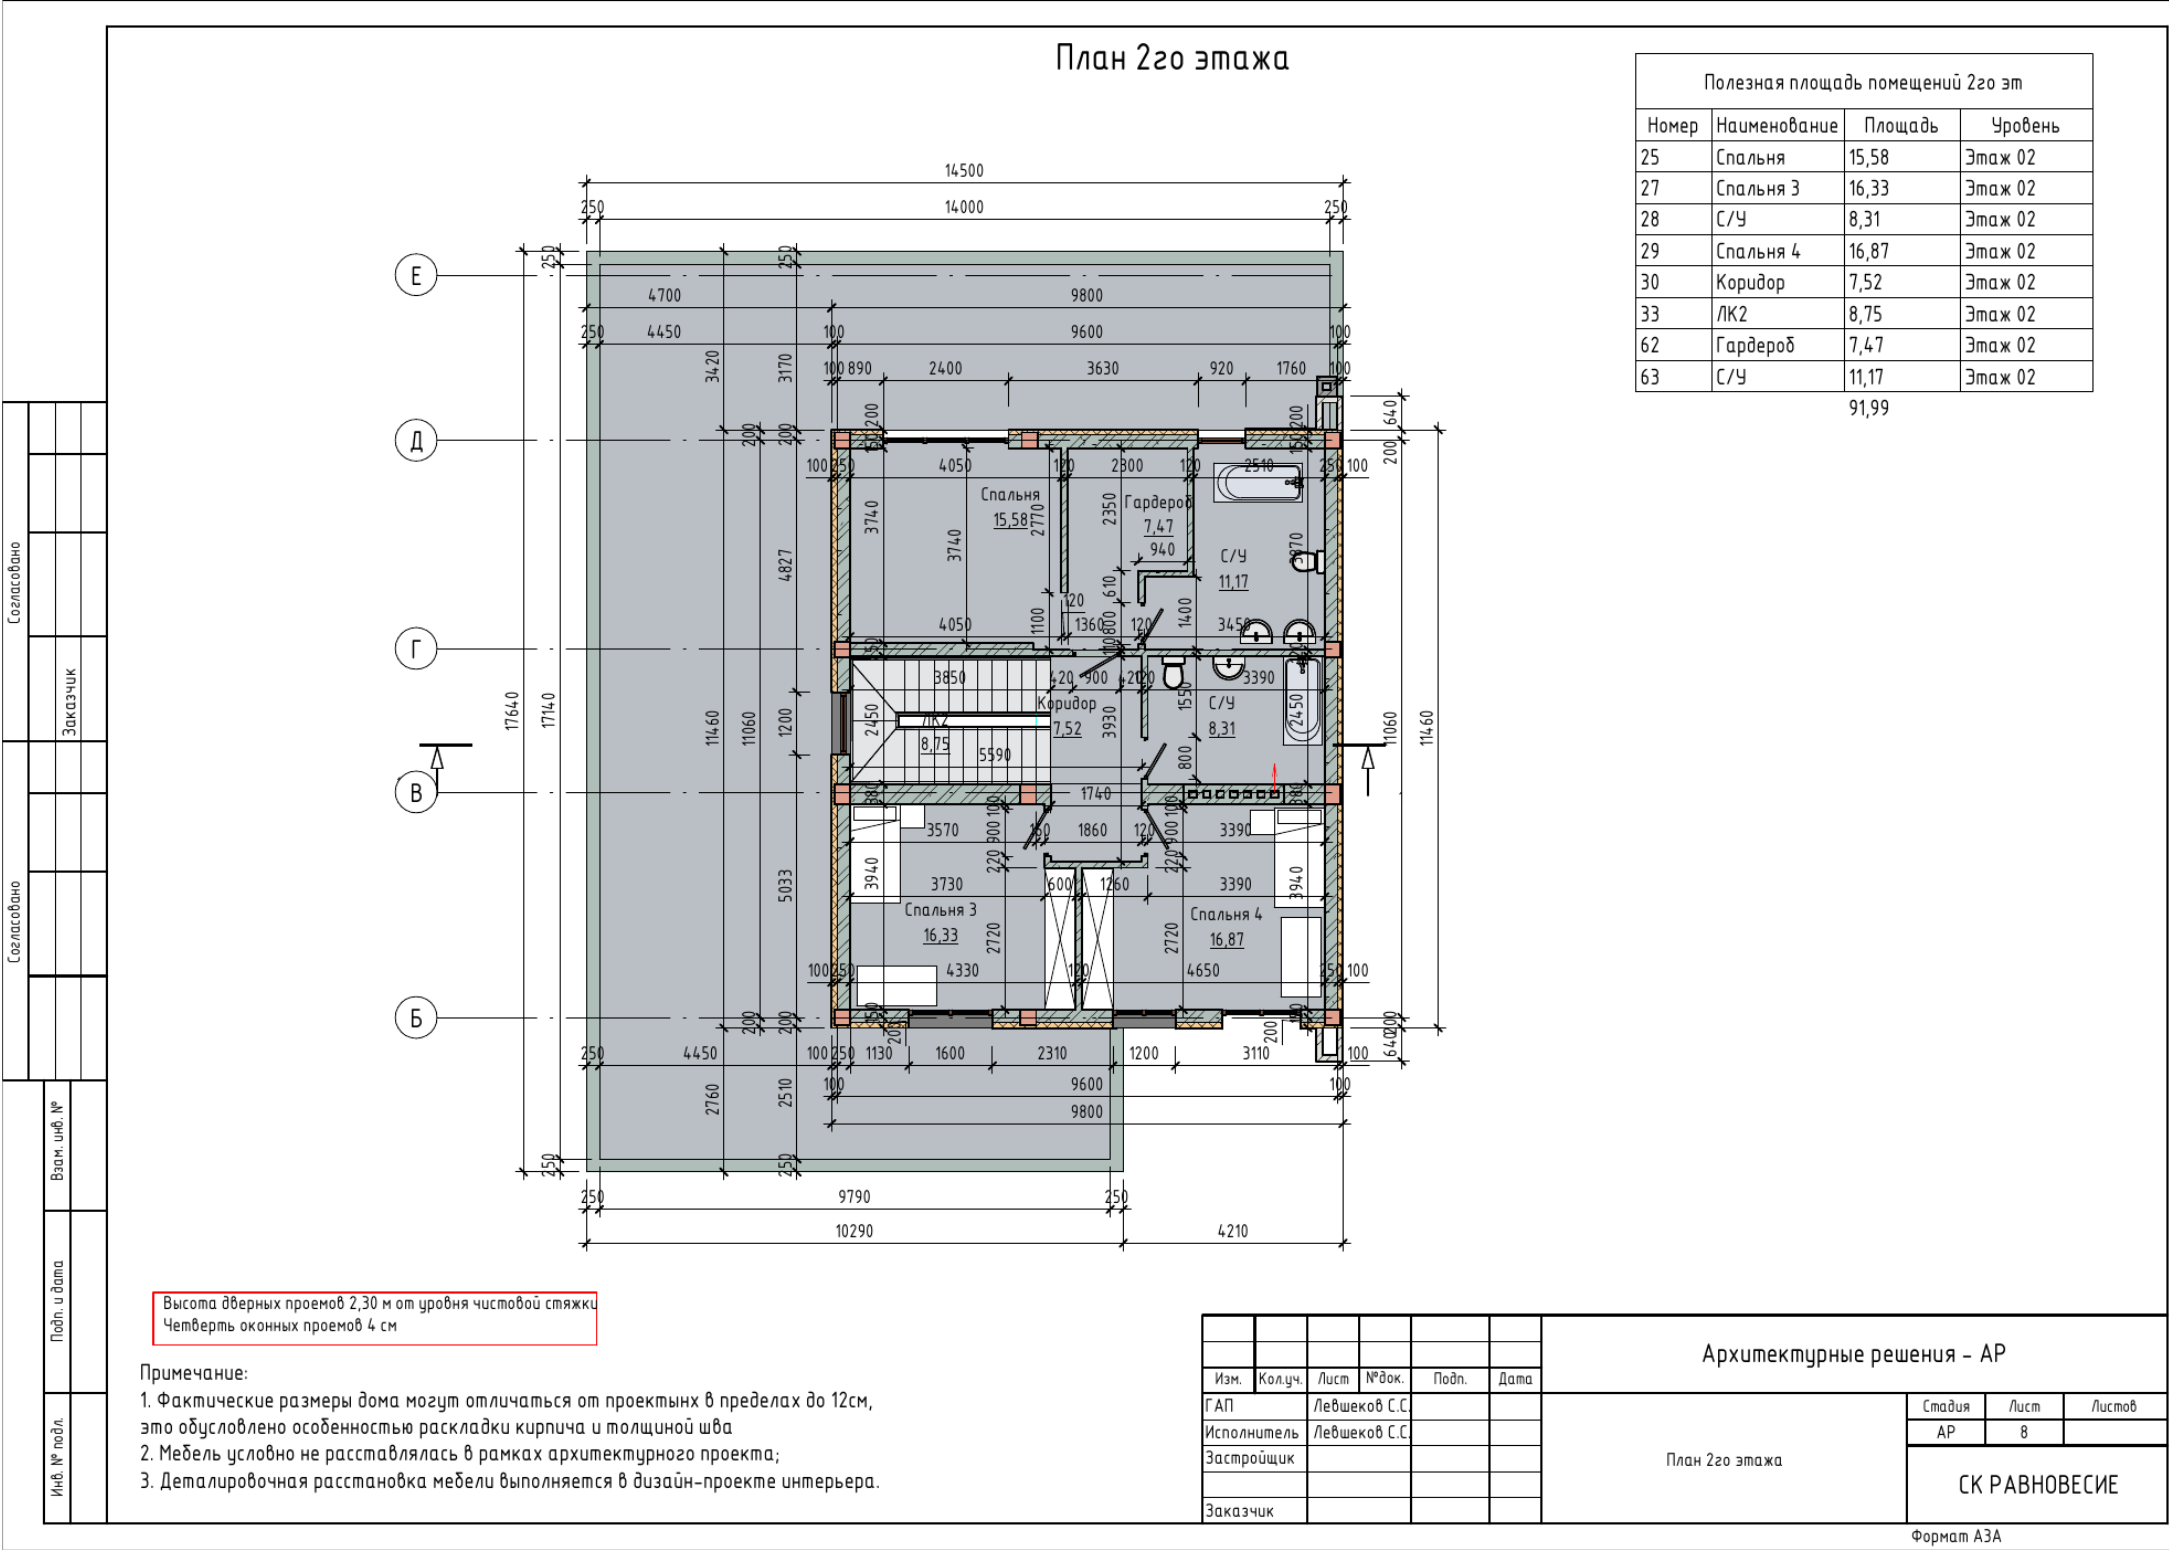

ПОДЛОЖКА ИЗ ИСХОДНОГО PDF. НЕ ИСПОЛНИТЕЛЬНЫЙ ОБМЕР. ГЕОМЕТРИЯ НЕ ПЕРЕРИСОВЫВАЛАСЬ.

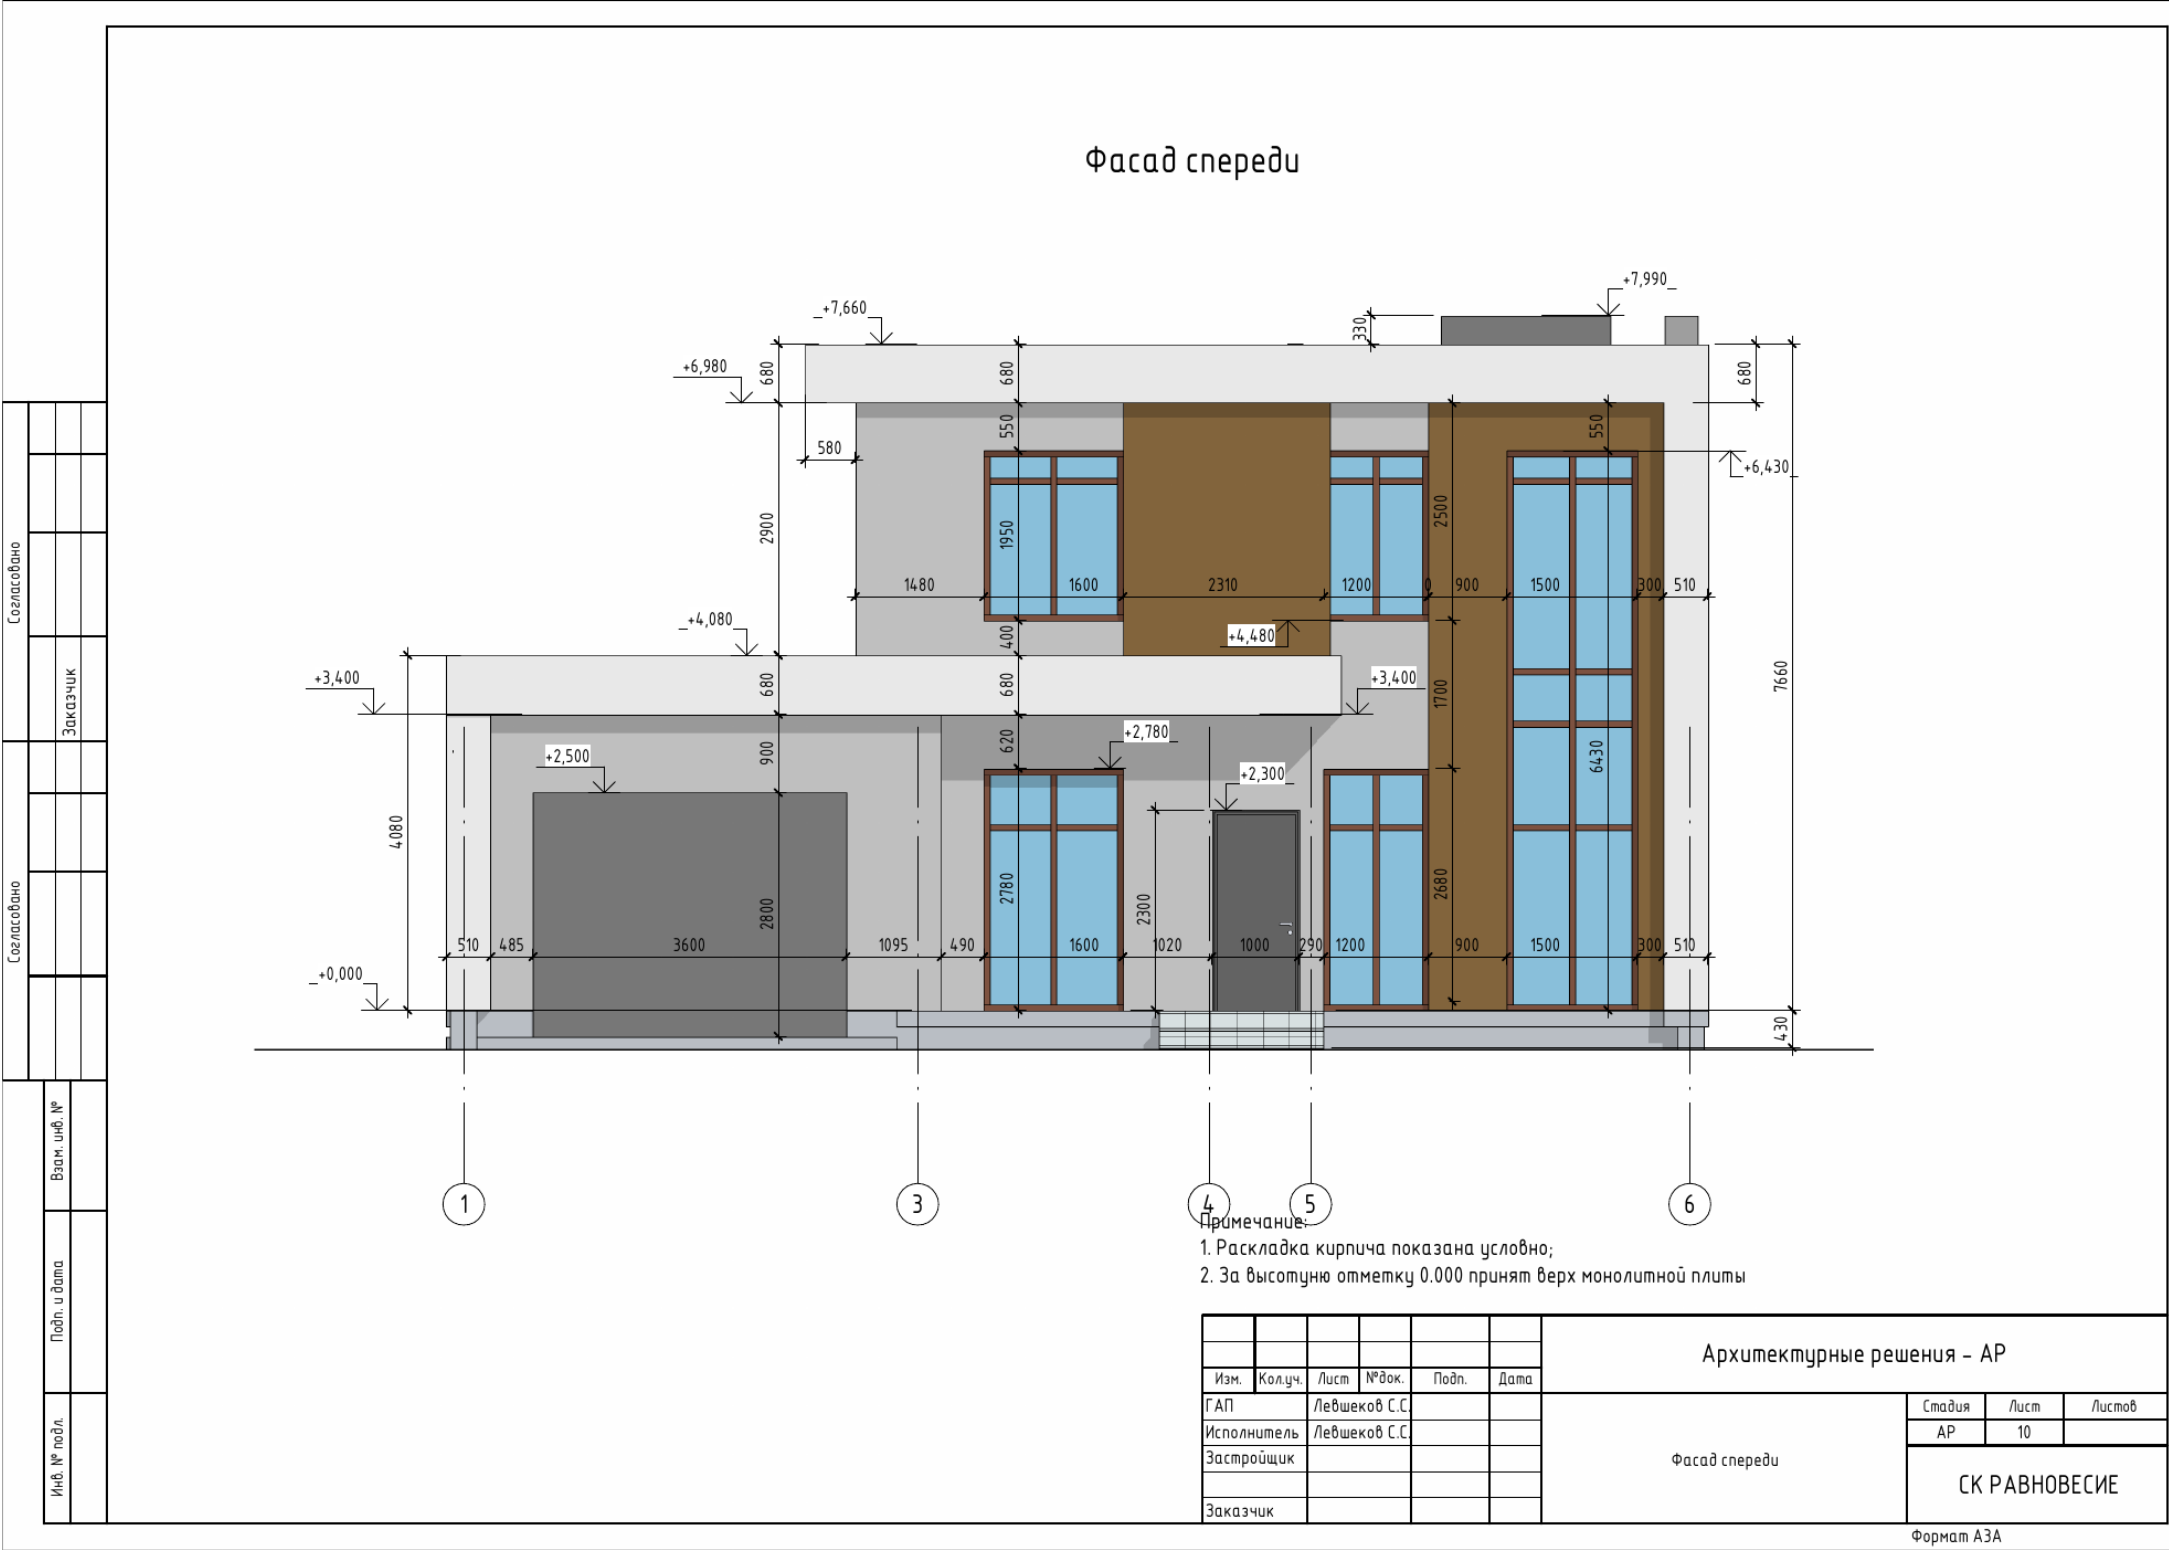

Михайличенко · Инженер ИИ

Фасад спереди

Разрез 1-1

Кровля плоская
 Верхнее покрытие - ПВХ мембрана 1,2мм эконоплат
 Геотекстиль
 Xps carbon prof slope (уклонообразующая прослойка)
 Xps carbon, 6 2 слоя (теплоизоляция)
 Пароизоляция
 Ж.б. плита покрытия, толщ. 180мм
 Отделка потолка

Отделка фасада
 Утеплитель - каменная вата - 100мм
 Кирпич керамический - 250 мм
 Внутренняя отделка

Кровля плоская
 Верхнее покрытие - ПВХ мембрана 1,2мм эконоплат
 Геотекстиль
 Xps carbon prof slope (уклонообразующая прослойка)
 Xps carbon, 6 2 слоя (теплоизоляция)
 Пароизоляция
 Ж.б. плита покрытия, толщ. 180мм
 Отделка потолка

Отделка фасада
 Утеплитель - каменная вата - 100мм
 Кирпич керамический - 250 мм
 Внутренняя отделка


Кровля плоская
 Верхнее покрытие - ПВХ мембрана 1,2мм эконоплат
 Геотекстиль
 Xps carbon prof slope (уклонообразующая прослойка)
 Xps carbon, 6 2 слоя (теплоизоляция)
 Пароизоляция
 Ж.б. плита покрытия, толщ. 180мм
 Отделка потолка

Отделка фасада
 Утеплитель - каменная вата - 100мм
 Кирпич керамический - 250 мм
 Внутренняя отделка


						Архитектурные решения – АР					
Изм.	Колуч.	Лист	№ док.	Подп.	Дата	Разрез 1-1	Стадия	Лист	Листов		
ГАП		Левшеков С.С.					АР	14			
Исполнитель		Левшеков С.С.					СК РАВНОВЕСИЕ				
Застройщик											
Подрядчик											

H1-AP-05 · H1-KOORD · 7/10 · по исходному листу

ОБЩИЙ БАЛКОН · ПЛАН И БЕЗОПАСНОСТЬ

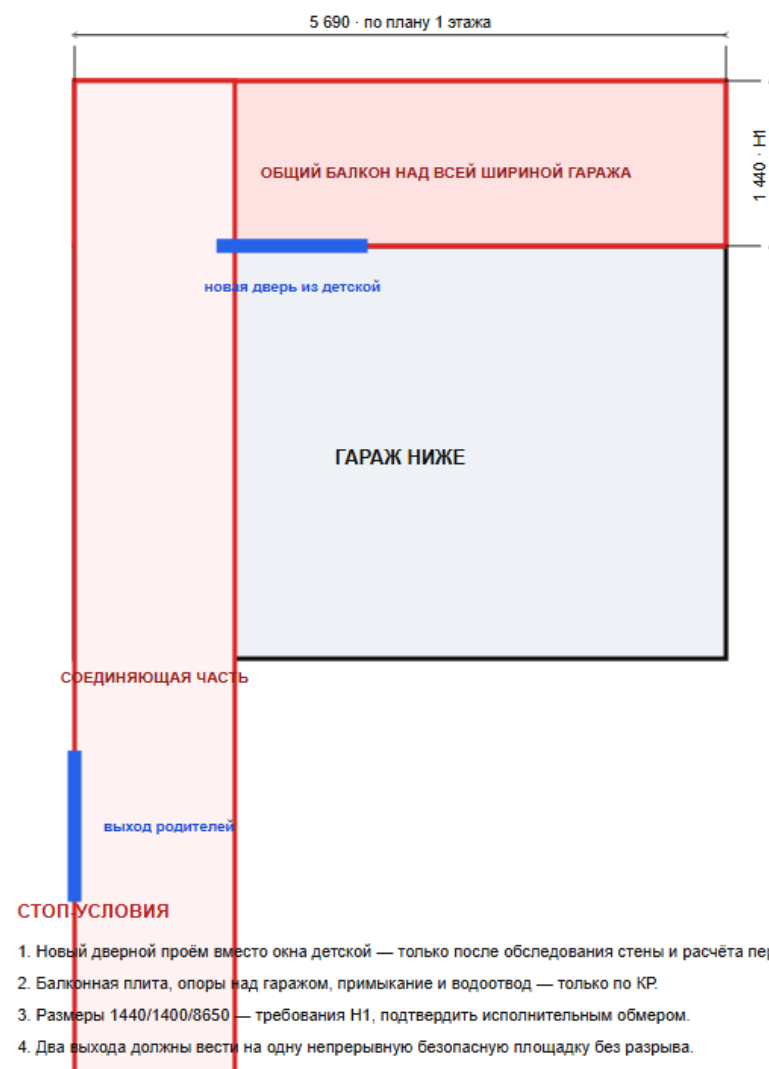

РАЗРЕЗ ОГРАЖДЕНИЯ · ТРЕБОВАНИЯ

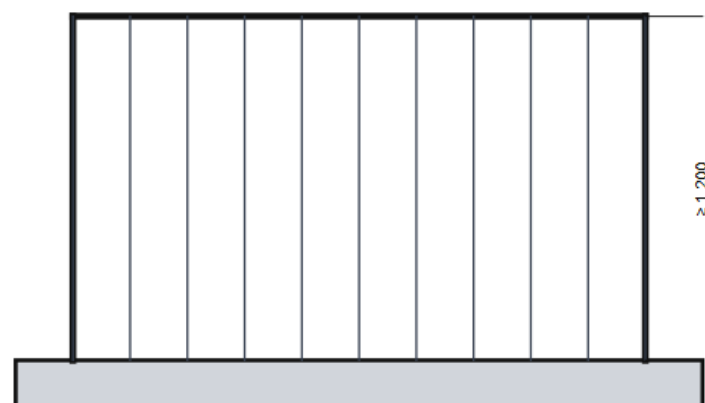

Шар/зазор заполнения ≤ 100 мм; горизонтальные элемен
облегчающие лазание детям, исключить. Узлы — по ра

ПРИМЕЧАНИЯ

Статус: ТРЕБУЕТ КОНСТРУКТОРА
Основание: PDF л.7–8 + изменение заказчика
Единицы линейных размеров: мм.
Размеры с PDF не заменяют исполнительный обмер.
Красный контур — новое/непровременное решение Н1.
До закрытия ворот G1–G7 лист не выдвигать в монтаж.

КООРДИНАЦИЯ. НЕ ДЛЯ МОНТАЖА. НУЖНЫ ОБМЕР, РАСЧЁТ И ПОДПИСИ ПРОФИЛЬНЫХ СПЕЦИАЛИСТОВ.	Михайличенко · Инженер ИИ	Масштаб: М 1:50
	Общий балкон над гаражом — схема изм...	Лист 8/10 · изм. 00
	Н1-АР-06 · стадия Н1-KOORD	Дата: 07.08.2026


Михайличенко · Инженер ИИ

Общий балкон над гаражом — схема изменения


H1-AP-06 · H1-KOORD · 8/10 · M 1:50

H1-BH-01 · H1-KOORD · 9/10 · M 1:50

МАНГАЛЬНАЯ · L-КОМПОНОВКА ПО ИСХОДНОМУ ПЛАНУ

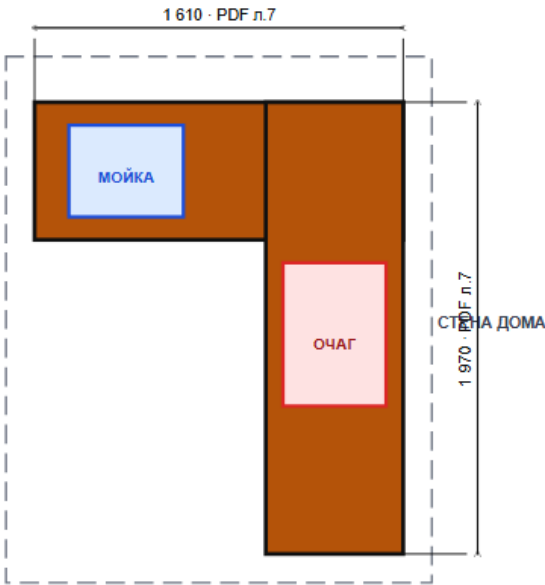

ФАСАД/РАЗВЁРТКА · ОКНО НЕ ПЕРЕКРЫВАТЬ

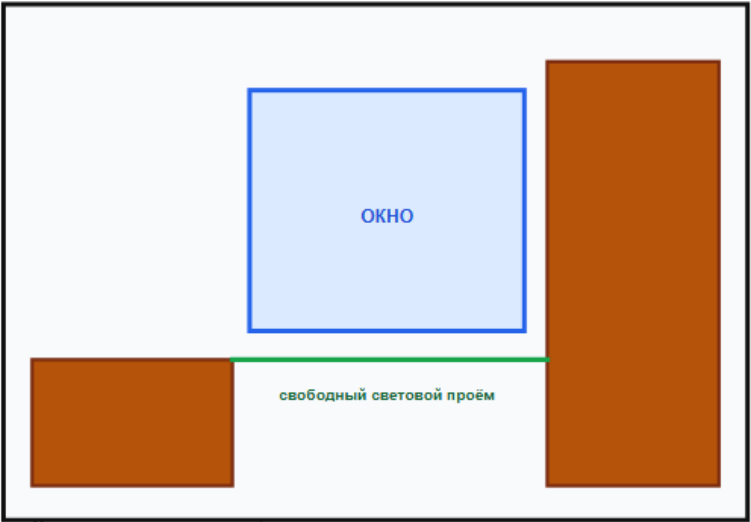

ПРИМЕЧАНИЯ

Статус: ТРЕБУЕТ ПЕЧНИКА/ОВ/ВК
Основание: PDF л.7 + фото заказчика
Единицы линейных размеров: мм.
Размеры с PDF не заменяют исполнительный обмер.
Красный контур — новое/непроверенное решение Н1.
До закрытия ворот G1–G7 лист не выдавать в монтаж.

ОБЯЗАТЕЛЬНЫЕ УЗЛЫ ДЛЯ РАБОЧЕГО ВЫПУСКА

1. Печник: топка, шамот, дымосборник, сечение и высота дымохода.
2. ОВ: независимый расчёт удаления дыма и притока; не использовать общедомовую вентиляцию.
3. ВК: мойка в столешнице, ХВС/ГВС, сифон, канализация, зимнее опорожнение.
4. КР: нагрузка кладки на плиту, примыкание к дому, деформационный/пожарный узел.
5. АР: координация окна, проходов, рабочей поверхности и негорючих облицовок.
6. ЭОМ: влагозащищённые розетки вне горячей зоны, свет и аварийное отключение.

Михайличенко · Инженер ИИ	Масштаб: М 1:25
Мангальная зона 1610 × 1970 — план и...	Лист 10/10 · изм. 00
Н1-TX-01 · стадия Н1-KOORD	Дата: 07.08.2026

Михайличенко · Инженер ИИ

Мангальная зона 1610 × 1970 — план и фасад

Н1-TX-01 · Н1-KOORD · 10/10 · М 1:25