


ЭОМ-01 · ПЕРВЫЙ ЭТАЖ · РОЗЕТКИ И ОСВЕЩЕНИЕ

ПРЕДВАРИТЕЛЬНОЕ ЗАДАНИЕ, НЕ РАБОЧИЙ ПРОЕКТ.
Привязки уточнить по обмеру, мебели, мощностям техники, ТУ и расчёту ЭОМ профильным проектировщиком.
14,50 м по исходному PDF

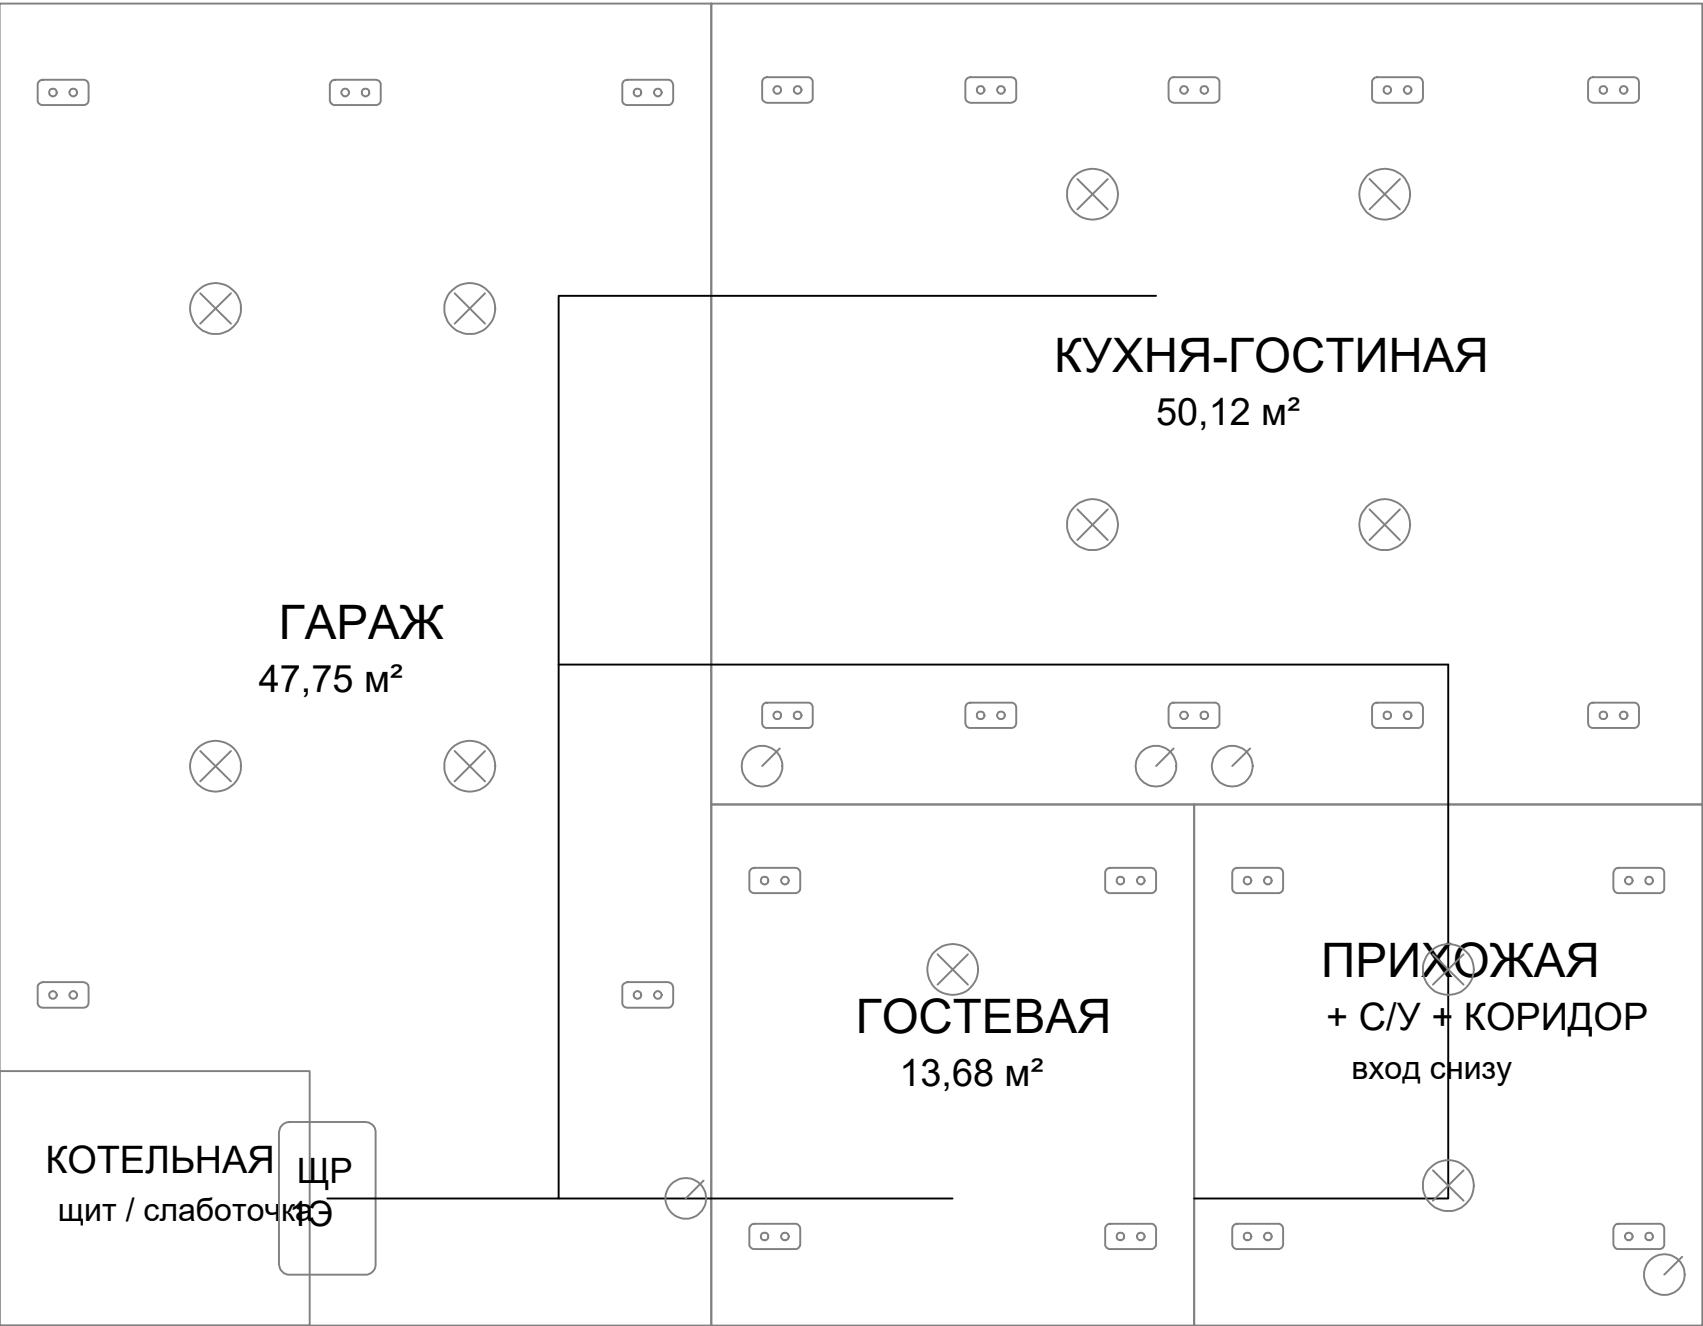

УСЛОВНЫЕ ОБОЗНАЧЕНИЯ

- розетка 230 В
- выключатель
- световая точка
- ЩР распределительный щит
- логика группы, не трасса

ОБЯЗАТЕЛЬНО УТОЧНИТЬ

- мощности варочной, духовки, ПММ;
- электромобиль / ворота / верстак;
- котёл, насосы, автоматика и резерв;
- высоты розеток по мебели;
- заземление, УЗО, СПД, селективность;
- отдельные линии мокрых зон.

Высоты-задание от чистого пола:
обычные розетки 300 мм; рабочая зона 1100 мм; выключатели 900 мм.
Финально — только после раскладки мебели.