



К-01. Котельная — координационная модель Cinema 4D v20.1
Единицы: мм · помещение на листе 7 PDF: 8,24 м² · модельная граница: 2450 × 2950 · окончательные чистовые размеры — после обмера

План, вид сверху

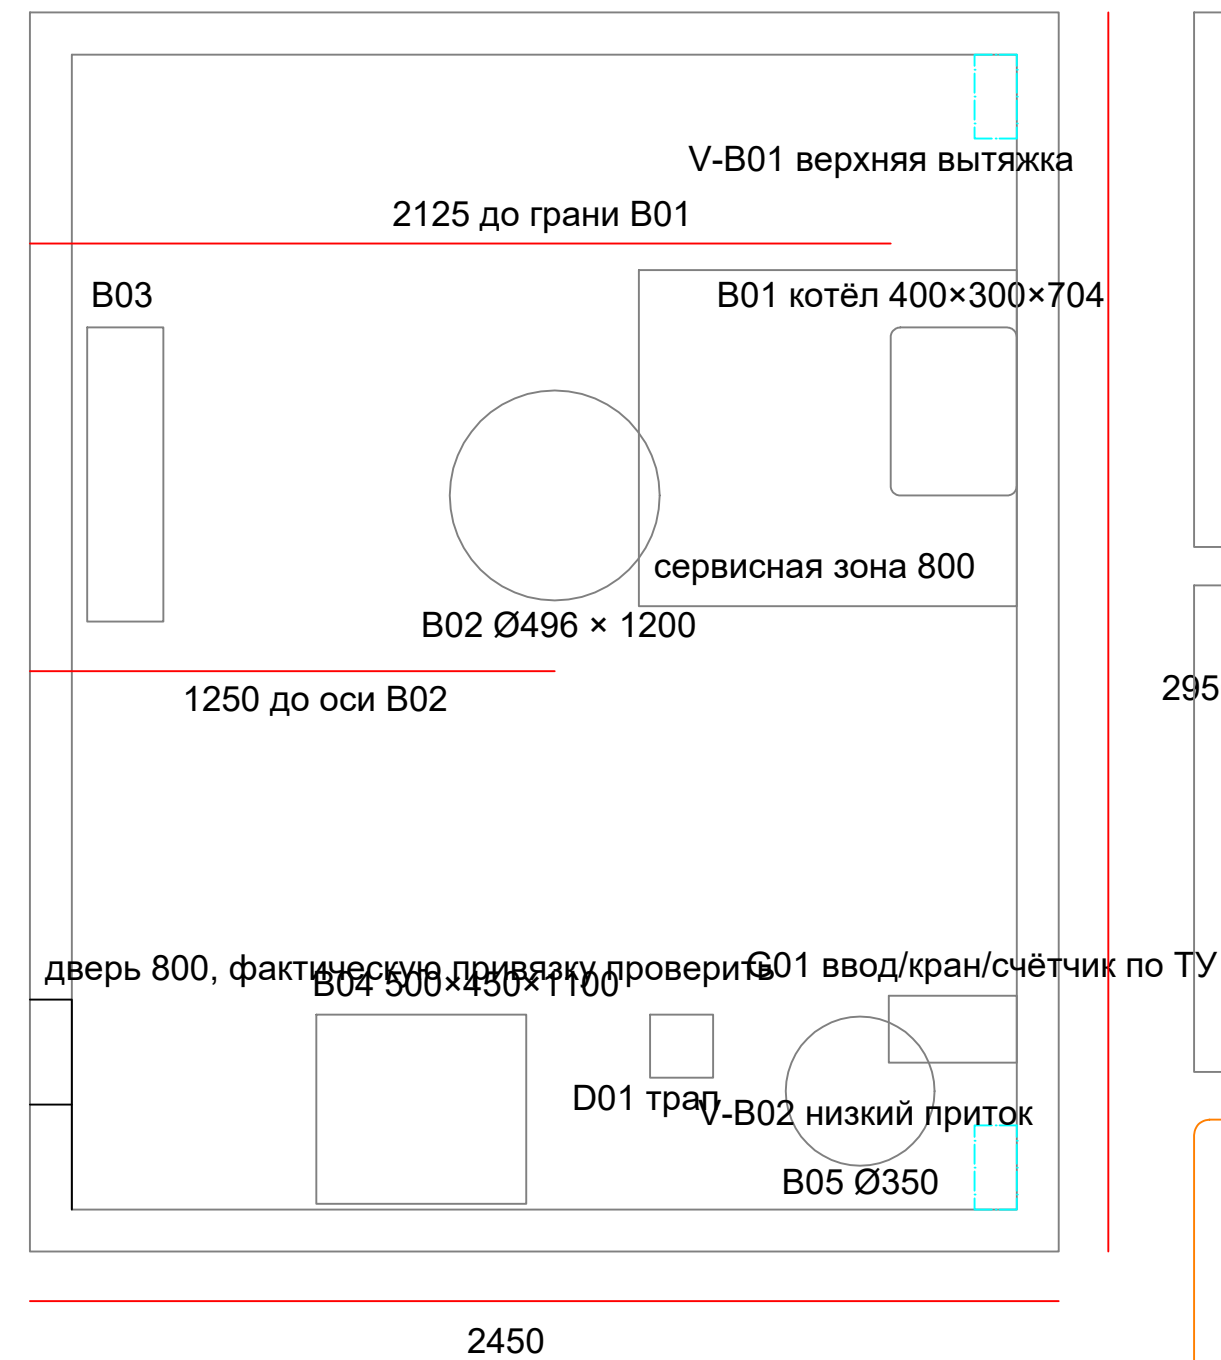

Развёртки стен — те же координаты C4D

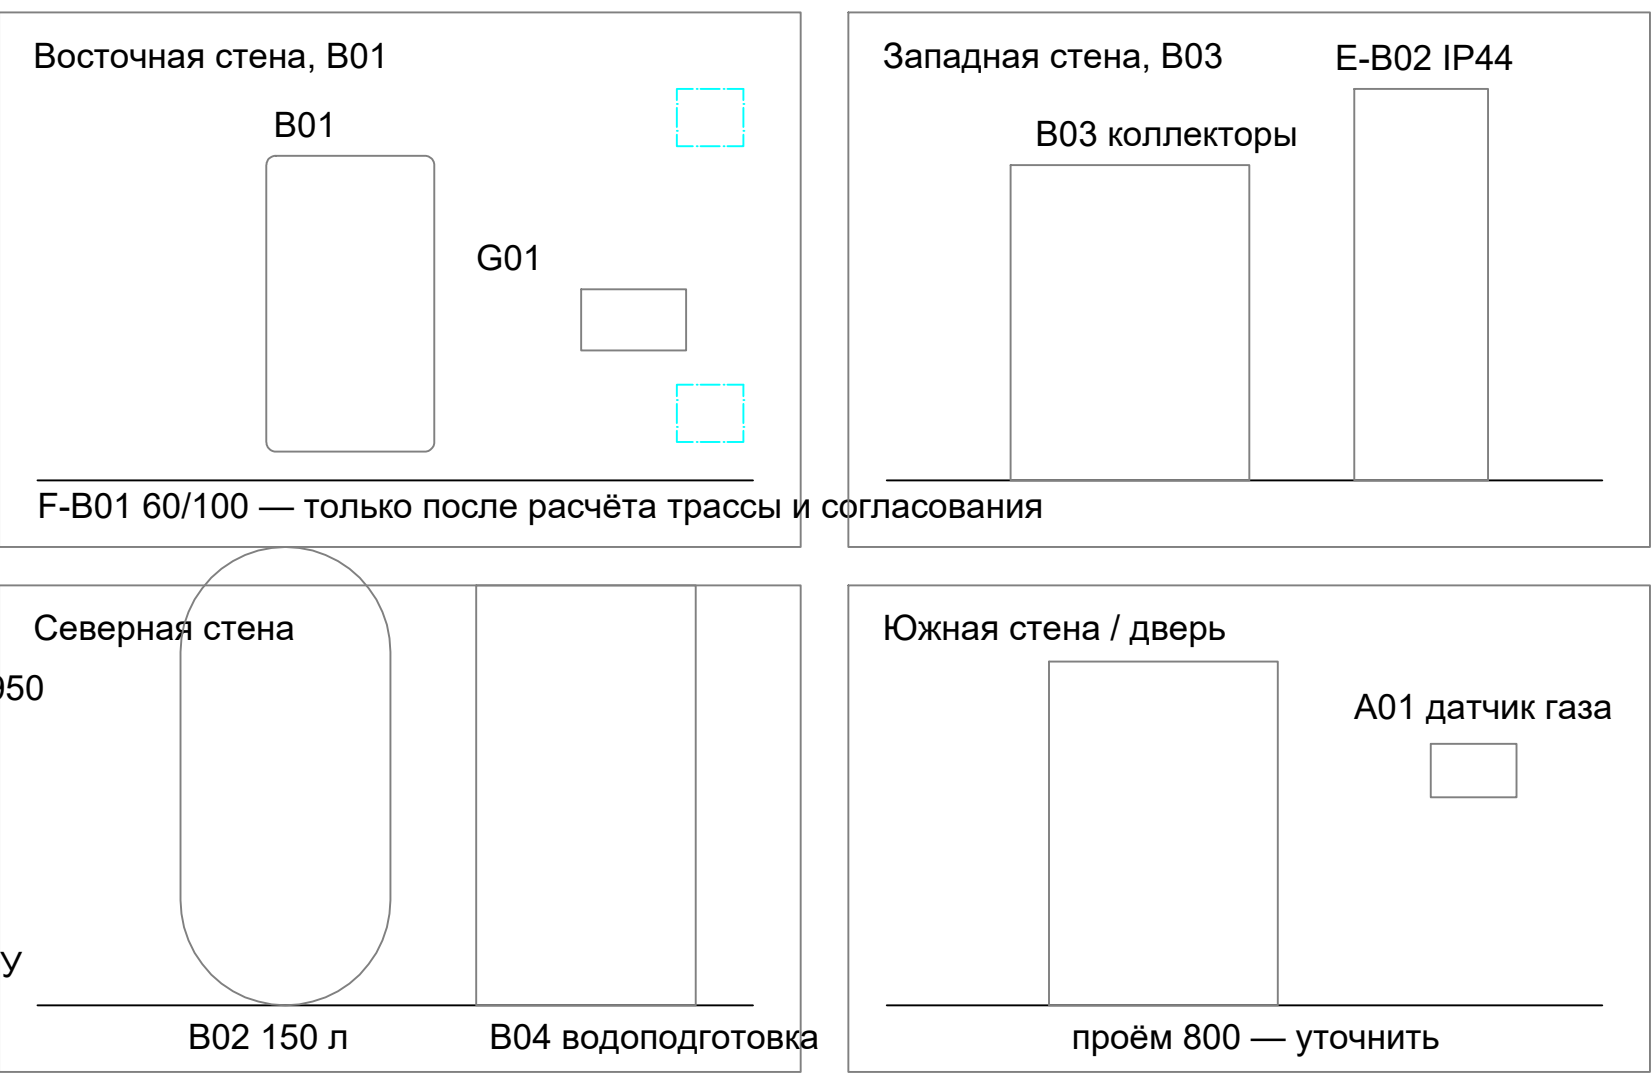

До передачи монтажнику обязательно получить

1. Технические условия на газ. 2. Теплотери и выбранную мощность. 3. Паспорт котла и схему дымоудаления.
4. Обмер помещения, окна/двери/высоту. 5. Расчёт воздухообмена. 6. Анализ воды. 7. Проект лицензирован.

B01 — официальная карточка BAXI ECO Nova 2025 1.24 F
B02 — официальная карточка ROMMER 150 л

Статус листа: КООРДИНАЦИЯ / ТЗ. Не рабочий проект газоснабжения и не разрешение на монтаж.